
ESTE DOCUMENTO NÃO PODE SER REPRODUZIDO, INTEGRAL OU PARCIALMENTE, POR QUALQUER MEIO, INCLUINDO FOTOCÓPIA, SEM AUTORIZAÇÃO

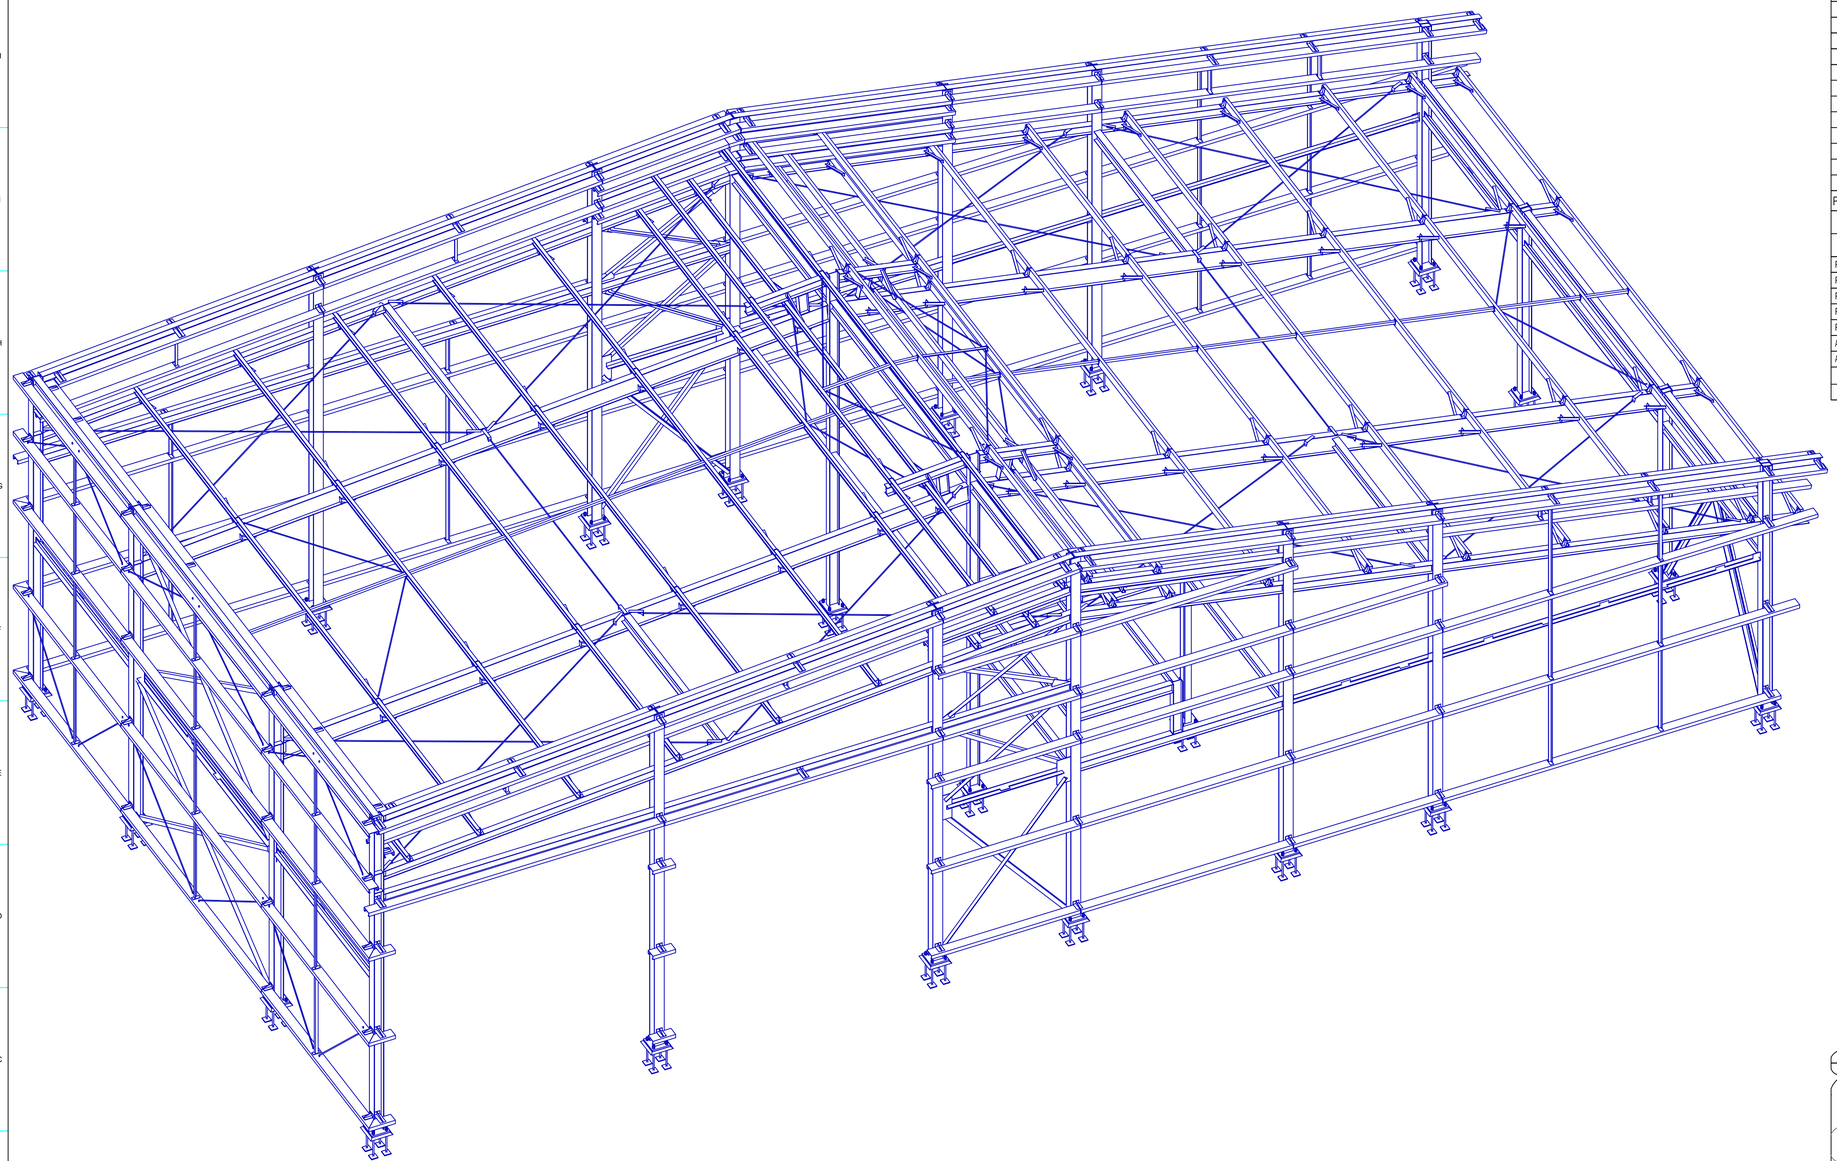

PERSPECTIVA

LISTA DE RESUMO DE MATERIAL

PERFIL	MATERIAL	QTD(mm/m²)	PESO (Kg)	SUP. (m²)
3/4"Ø_HEAVY_HEX_NUT	A325	6384	33.6	1.5
3/4"Ø_WASHER	A36	336	0.0	0.2
BARRA.RED.12.7	A36	100597	99.2	3.9
BARRA.RED.19	A36	40404	92.4	2.4
C100X50X17X2	A36	250987	871.7	114.5
C150X60X20X3	A36	389640	2664.8	234.2
D12.5	SAE_1020	60536	52.6	2.3
L40X40X2	A36	70014	86.4	11.2
L40X40X3.25	A36	68530	132.4	11.0
L64X4.8	A572-GR.50	143856	657.5	36.6
L100X50X3.25	A36	8280	27.6	2.6
L130X50X3.25	A36	9720	43.2	3.6
L203X50X3.25	A36	5940	39.6	3.1
W150X13	A572-GR.50	215131	2795.9	144.1
W150X18	A572-GR.50	11890	214.0	8.2
W150X22.5	A572-GR.50	97273	2188.4	85.6
W310X21	A572-GR.50	43069	904.4	42.2
CH. 3.3	A36	2.86	95.4	6.3
CH. 4.8	A36	0.16	6.0	0.3
CH. 6.0	A36	0.15	8.2	0.3
CH. 6.4	A36	1.81	102.0	3.9
CH. 8.0	A36	0.75	46.0	1.8
CH. 10.0	A36	0.84	67.2	2.0
CH. 25.0	A36	1.67	327.6	3.9
PESO TOTAL: 11556.1 Kg		SUPERFICE A TRATAR: 726.0 m²		

LISTA DE PARAFUSOS

DESCRIÇÃO	NORMA	CLASSE	QTD.	PESO
PARAF. Ø1/2" X 1 1/2"	ASTM	A325N	18	0.74
PARAF. Ø1/2" X 1 1/4"	ASTM	A325N	371	18.92
PARAF. Ø3/8" X 1"	ASTM	A325N	1568	32.93
PORCA Ø1/2"	ASTM	A563 DH	389	7.00
PORCA Ø3/8"	ASTM	A563 DH	1568	12.54
ARRUELA Ø1/2"	ASTM	F436	389	1.95
ARRUELA Ø3/8"	ASTM	F436	1568	7.84
		PESO TOTAL		81.92

REV.	DATA	REVISOR	OBSERVAÇÕES
00	15/04/26	HELEN KÁSSIA	EMISSÃO INICIAL

STRUCKSTEEL
ESTRUTURAS METÁLICAS
struckssteelestruturasmetalicas@gmail.com

POSTO OPERACIONAL HIDROLÂNDIA

PROPRIETÁRIO: CORPO DE BOMBEIROS MILITAR DE GOIÁS- CNPJ 33.638.099/0001-00

PROJETISTA: ENGº. JOÃO PEDRO GUIMARÃES BATISTELA - CREA 101.831.1009/D-GO


DESENHISTA: ENGª. HELEN KÁSSIA PEREIRA SILVA - CREA 101.916.4573/D-GO

PROJETO ELABORADO SEGUINDO NORMAS VIGENTES - NBR8800:2024 (PERFIS LAMINADOS), NBR14762:2010 (PERFIS FORMADOS A FRIO), NBR6123:2023 (AÇÃO DO VENTO) E NBR8120:2016 (SOBRECARGA DE USO).


TÍTULO: PERSPECTIVA

FORMATO: A1	ARQUIVO: PA-2604-POH-01-R00		Nº PROJETO	REVISÃO
ESCALA: 1:40	DATA: 16/04/26	PÁGINA: 1	2604	00


ESTE DOCUMENTO NÃO PODE SER REPRODUZIDO, INTEGRAL OU PARCIALMENTE, POR QUALQUER MEIO, INCLUINDO FOTOCÓPIA, SEM AUTORIZAÇÃO

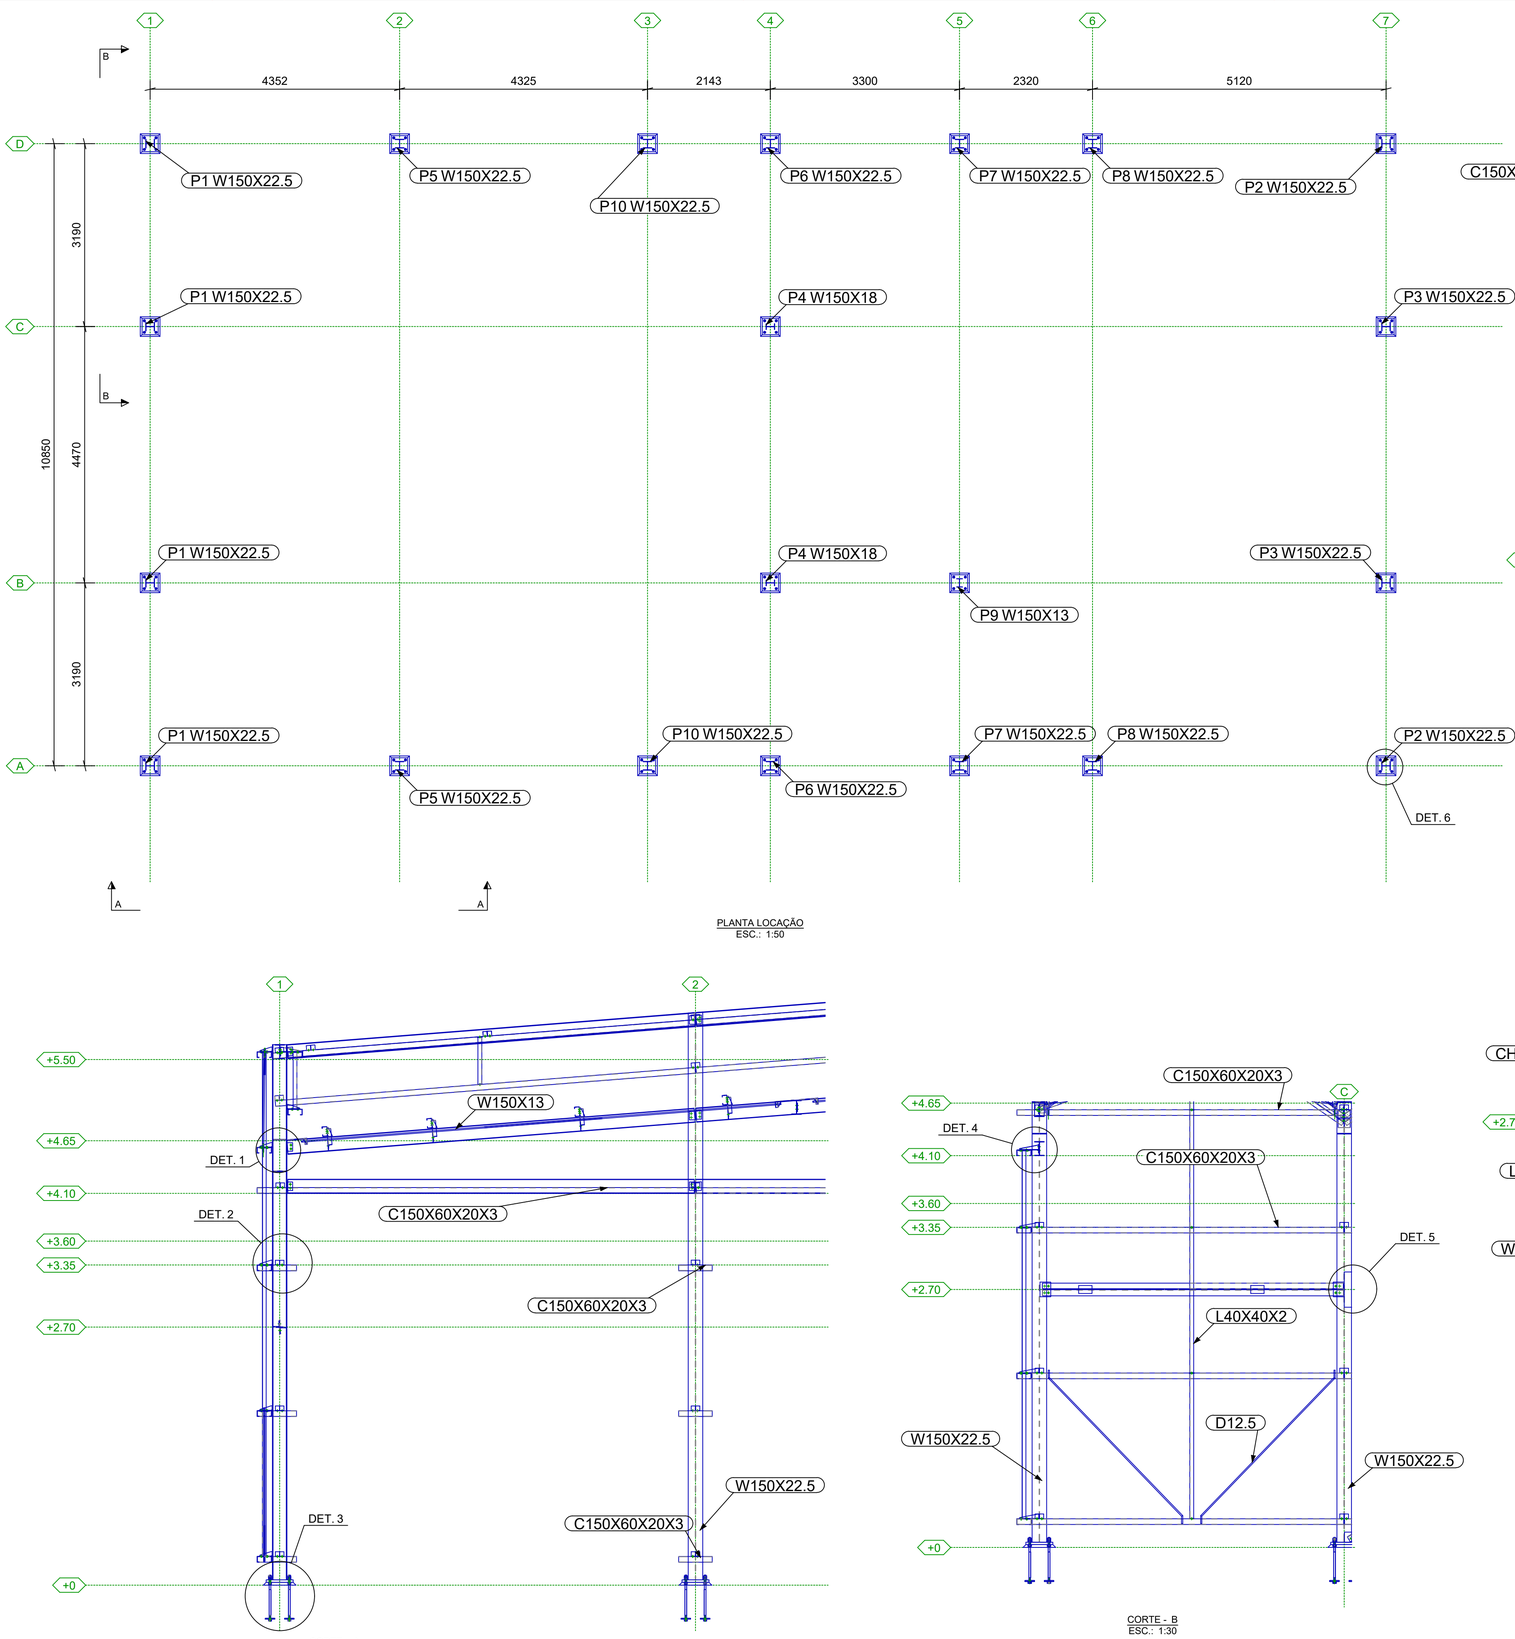


PLANTA LOCAÇÃO
ESC.: 1:50

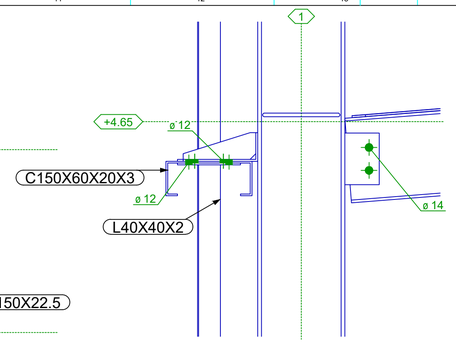


DETALHE - 1
ESC.: 1:5

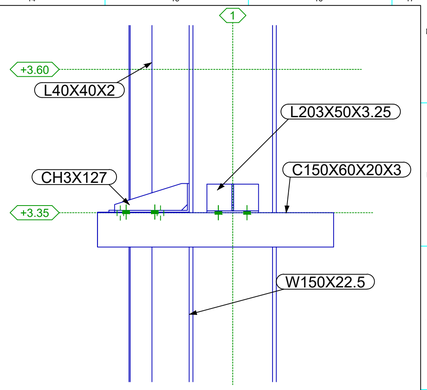

DETALHE - 2
ESC.: 1:5

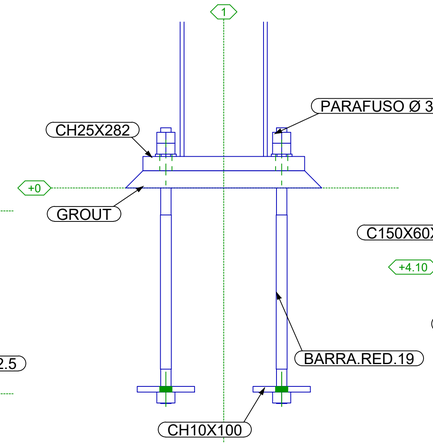


DETALHE - 3
ESC.: 1:5

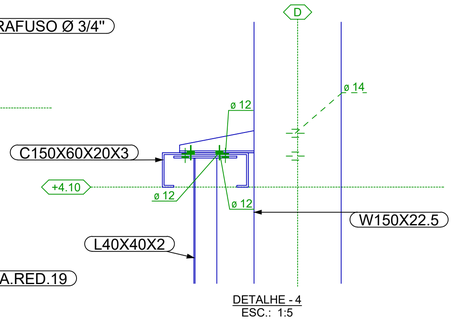


DETALHE - 4
ESC.: 1:5

CORTE - A
ESC.: 1:30

CORTE - B
ESC.: 1:30

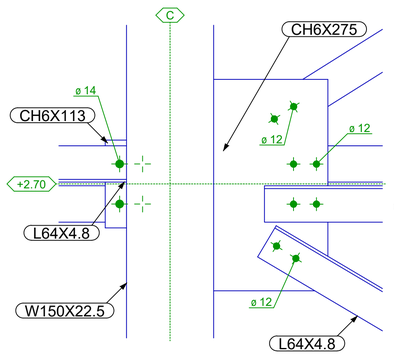

DETALHE - 5
ESC.: 1:5

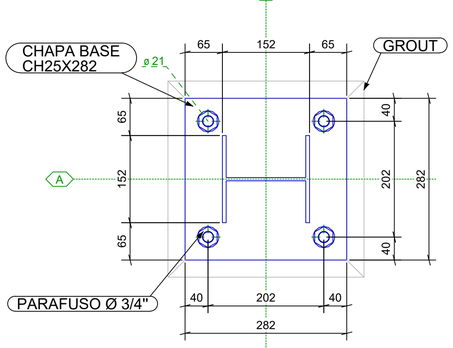

DETALHE - 6
ESC.: 1:5

REV.	DATA	REVISOR	OBSERVAÇÕES
00	15/04/26	HELEN KÁSSIA	EMISSÃO INICIAL

STRUCKSTEEL

ESTRUTURAS METÁLICAS
struckssteelestruturasmetalicas@gmail.com

POSTO OPERACIONAL HIDROLÂNDIA

PROPRIETÁRIO:

PROJETISTA: CORPO DE BOMBEIROS MILITAR DE GOIÁS- CNPJ 33.638.099/0001-00

DESENHISTA: ENGº. JOÃO PEDRO GUIMARÃES BATISTELA - CREA 101.831.1009/D-GO


ENGª. HELEN KÁSSIA PEREIRA SILVA - CREA 101.916.4573/D-GO

PROJETO ELABORADO SEGUINDO NORMAS VIGENTES - NBR8800:2024 (PERFIS LAMINADOS), NBR14762:2010 (PERFIS FORMADOS A FRIO), NBR6123:2023 (AÇÃO DO VENTO) E NBR8120:2016 (SOBRECARGA DE USO)

TÍTULO: PLANTA DE LOCAÇÃO

FORMATO: A1	ARQUIVO: PA-2604-POH-01-R00		Nº PROJETO	REVISÃO
ESCALA: 1:5	DATA: 16/04/26	PÁGINA: 2	2604	00

ESTE DOCUMENTO NÃO PODE SER REPRODUZIDO, INTEGRAL OU PARCIALMENTE, POR QUALQUER MEIO, INCLUINDO FOTOCÓPIA, SEM AUTORIZAÇÃO

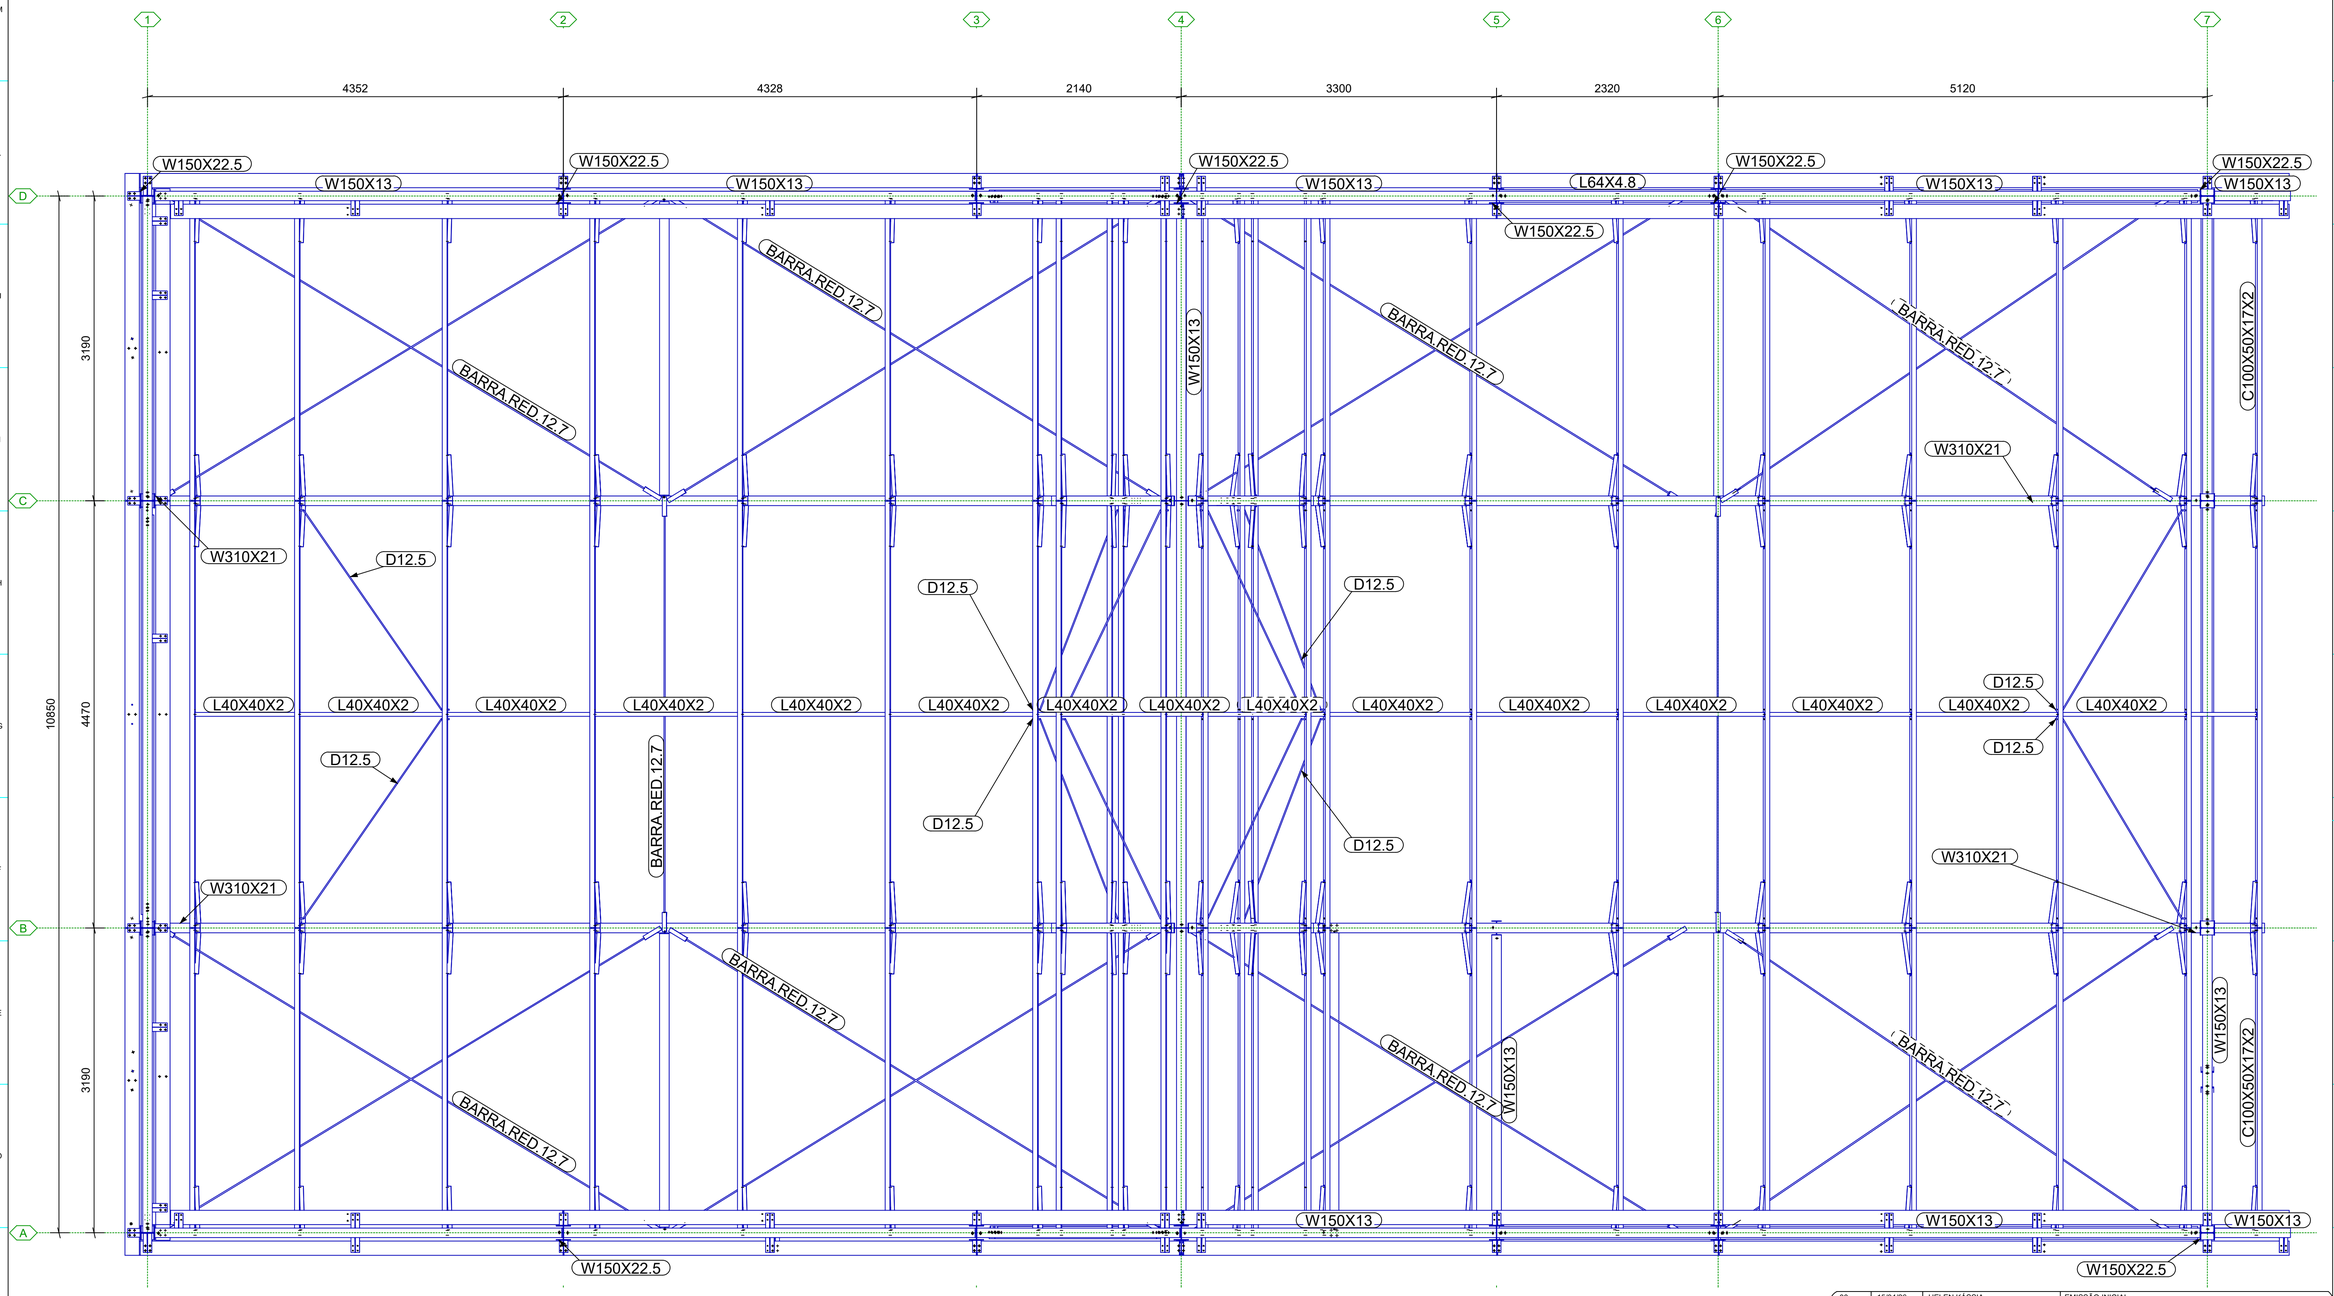

PLANTA DE COBERTURA
ESC.: 1:30

REV.	DATA	REVISOR	OBSERVAÇÕES
00	15/04/26	HELEN KÁSSIA	EMISSÃO INICIAL

STRUCKSTEEL
ESTRUTURAS METÁLICAS
strucksteelestruturasmetalicas@gmail.com

POSTO OPERACIONAL HIDROLÂNDIA

PROPRIETÁRIO:

PROJETISTA: CORPO DE BOMBEIROS MILITAR DE GOIÁS- CNPJ 33.638.099/0001-00

ENGº. JOÃO PEDRO GUIMARÃES BATISTELA - CREA 101.831.1009/D-GO

DESENHISTA:


ENGª. HELEN KÁSSIA PEREIRA SILVA - CREA 101.916.4573/D-GO

PROJETO ELABORADO SEGUINDO NORMAS VIGENTES - NBR8800:2024 (PERFIS LAMINADOS), NBR14762:2010 (PERFIS FORMADOS A FRIO), NBR6123:2023 (AÇÃO DO VENTO) E NBR8120:2016 (SOBRECARGA DE USO)

TÍTULO: PLANTA DE COBERTURA

FORMATO: A1	ARQUIVO: PA-2604-POH-01-R00		Nº PROJETO	REVISÃO
ESCALA: 1:30	DATA: 16/04/26	PÁGINA: 3	2604	00

ESTE DOCUMENTO NÃO PODE SER REPRODUZIDO, INTEGRAL OU PARCIALMENTE, POR QUALQUER MEIO, INCLUINDO FOTOCÓPIA, SEM AUTORIZAÇÃO

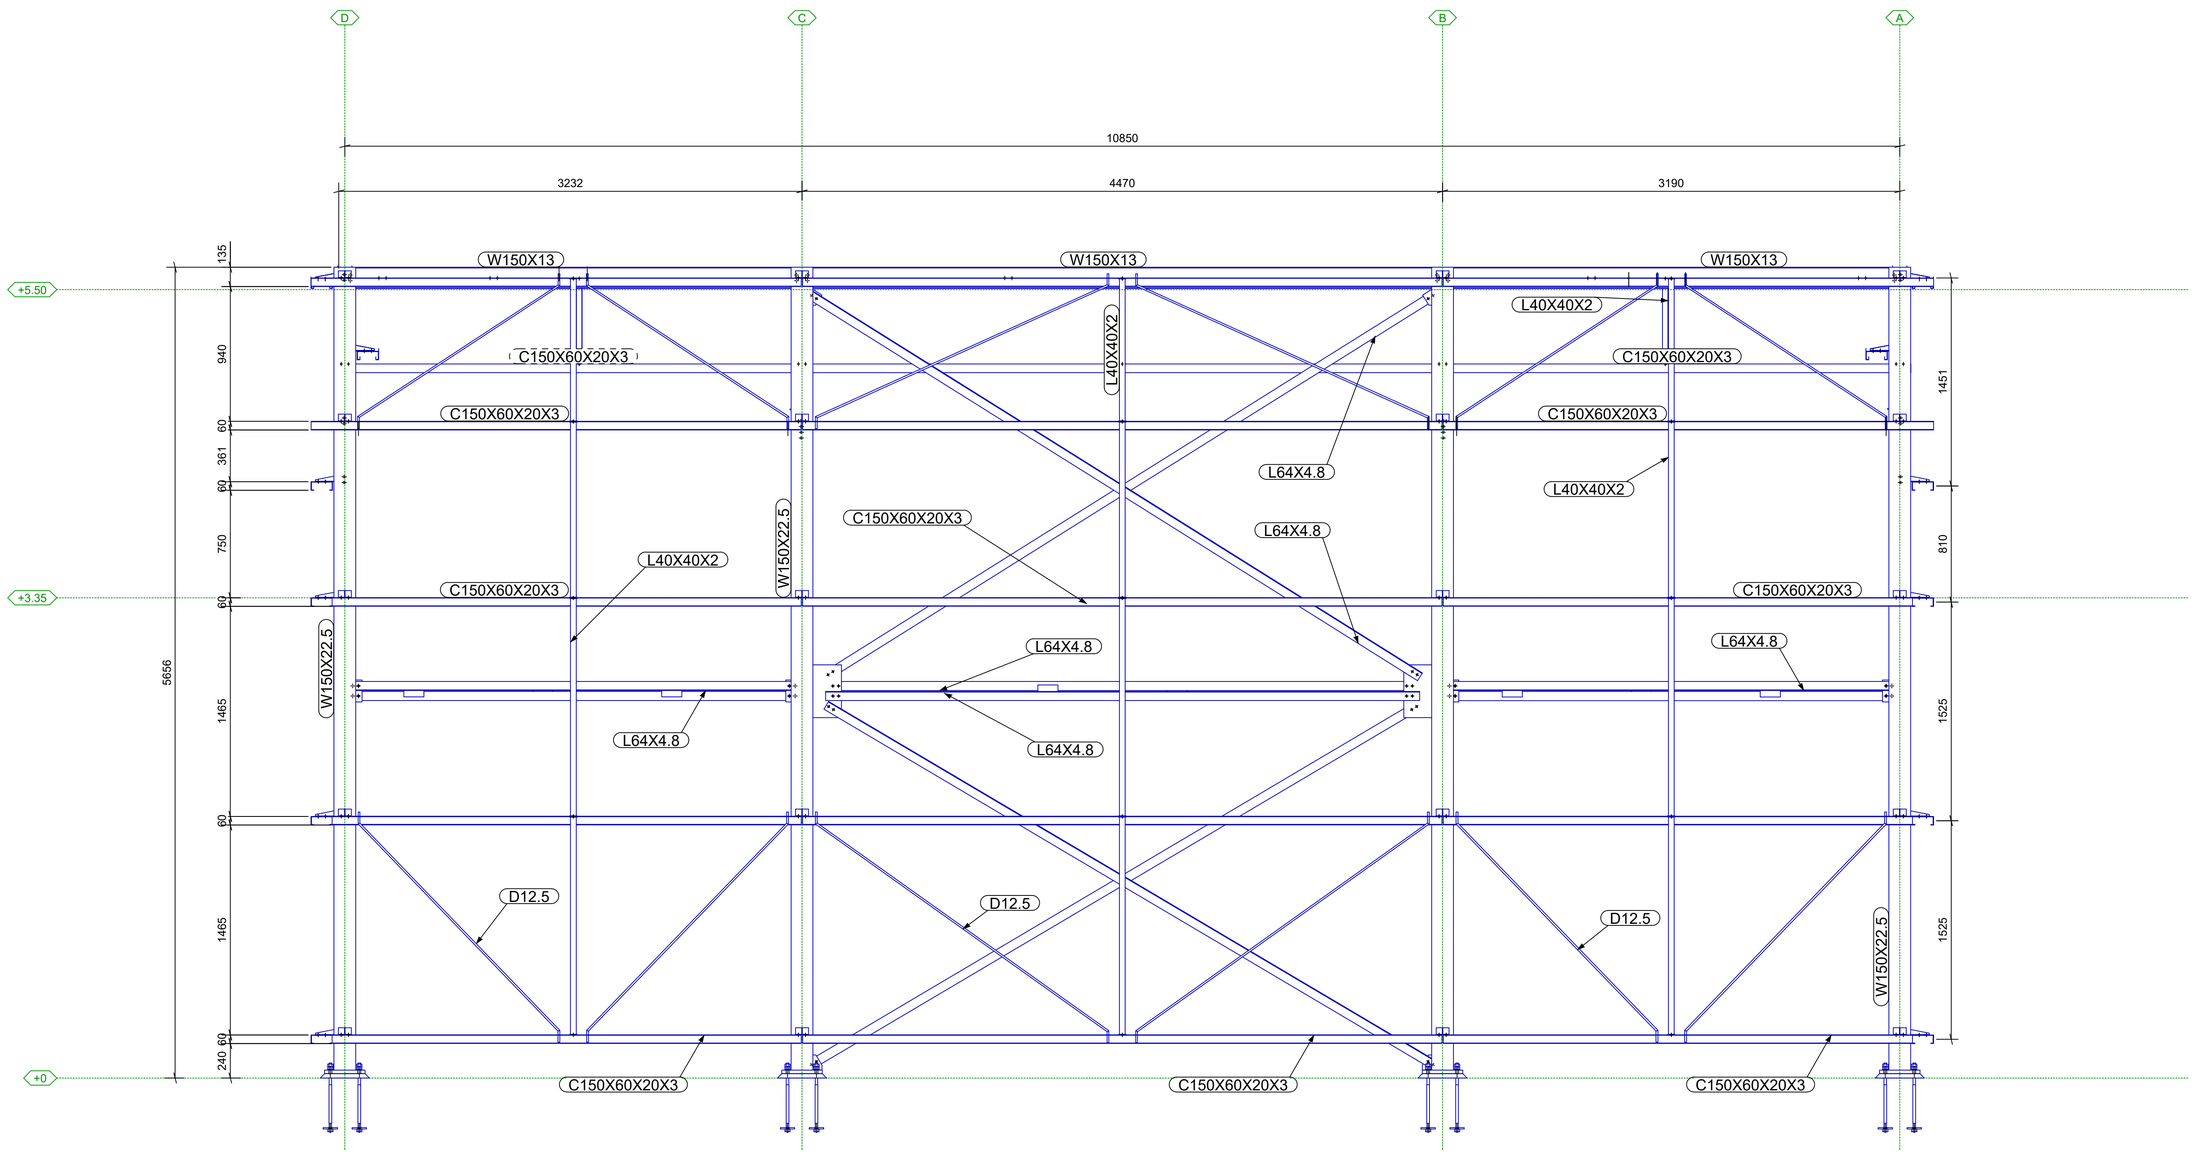

EIXO 1
ESC.: 1:20

REV.	DATA	REVISOR	OBSERVAÇÕES
00	15/04/26	HELEN KÁSSIA	EMISSÃO INICIAL

STRUCKSTEEL
ESTRUTURAS METÁLICAS
struckssteelestruturasmetalicas@gmail.com

POSTO OPERACIONAL HIDROLÂNDIA

PROPRIETÁRIO:

PROJETISTA: CORPO DE BOMBEIROS MILITAR DE GOIÁS- CNPJ 33.638.099/0001-00

ENGº. JOÃO PEDRO GUIMARÃES BATISTELA - CREA 101.831.1009/D-GO

DESENHISTA:


ENGª. HELEN KÁSSIA PEREIRA SILVA - CREA 101.916.4573/D-GO

PROJETO ELABORADO SEGUINDO NORMAS VIGENTES - NBR8800:2024 (PERFIS LAMINADOS), NBR14762:2010 (PERFIS FORMADOS A FRIO), NBR6123:2023 (AÇÃO DO VENTO) E NBR8400:2019 (SOBRECARGA DE USO).

TÍTULO: EIXO 1

FORMATO: A1	ARQUIVO: PA-2604-POH-01-R00		Nº PROJETO	REVISÃO
ESCALA: 1:20	DATA: 16/04/26	PÁGINA: 4	2604	00

ESTE DOCUMENTO NÃO PODE SER REPRODUZIDO, INTEGRAL OU PARCIALMENTE, POR QUALQUER MEIO, INCLUINDO FOTOCÓPIA, SEM AUTORIZAÇÃO

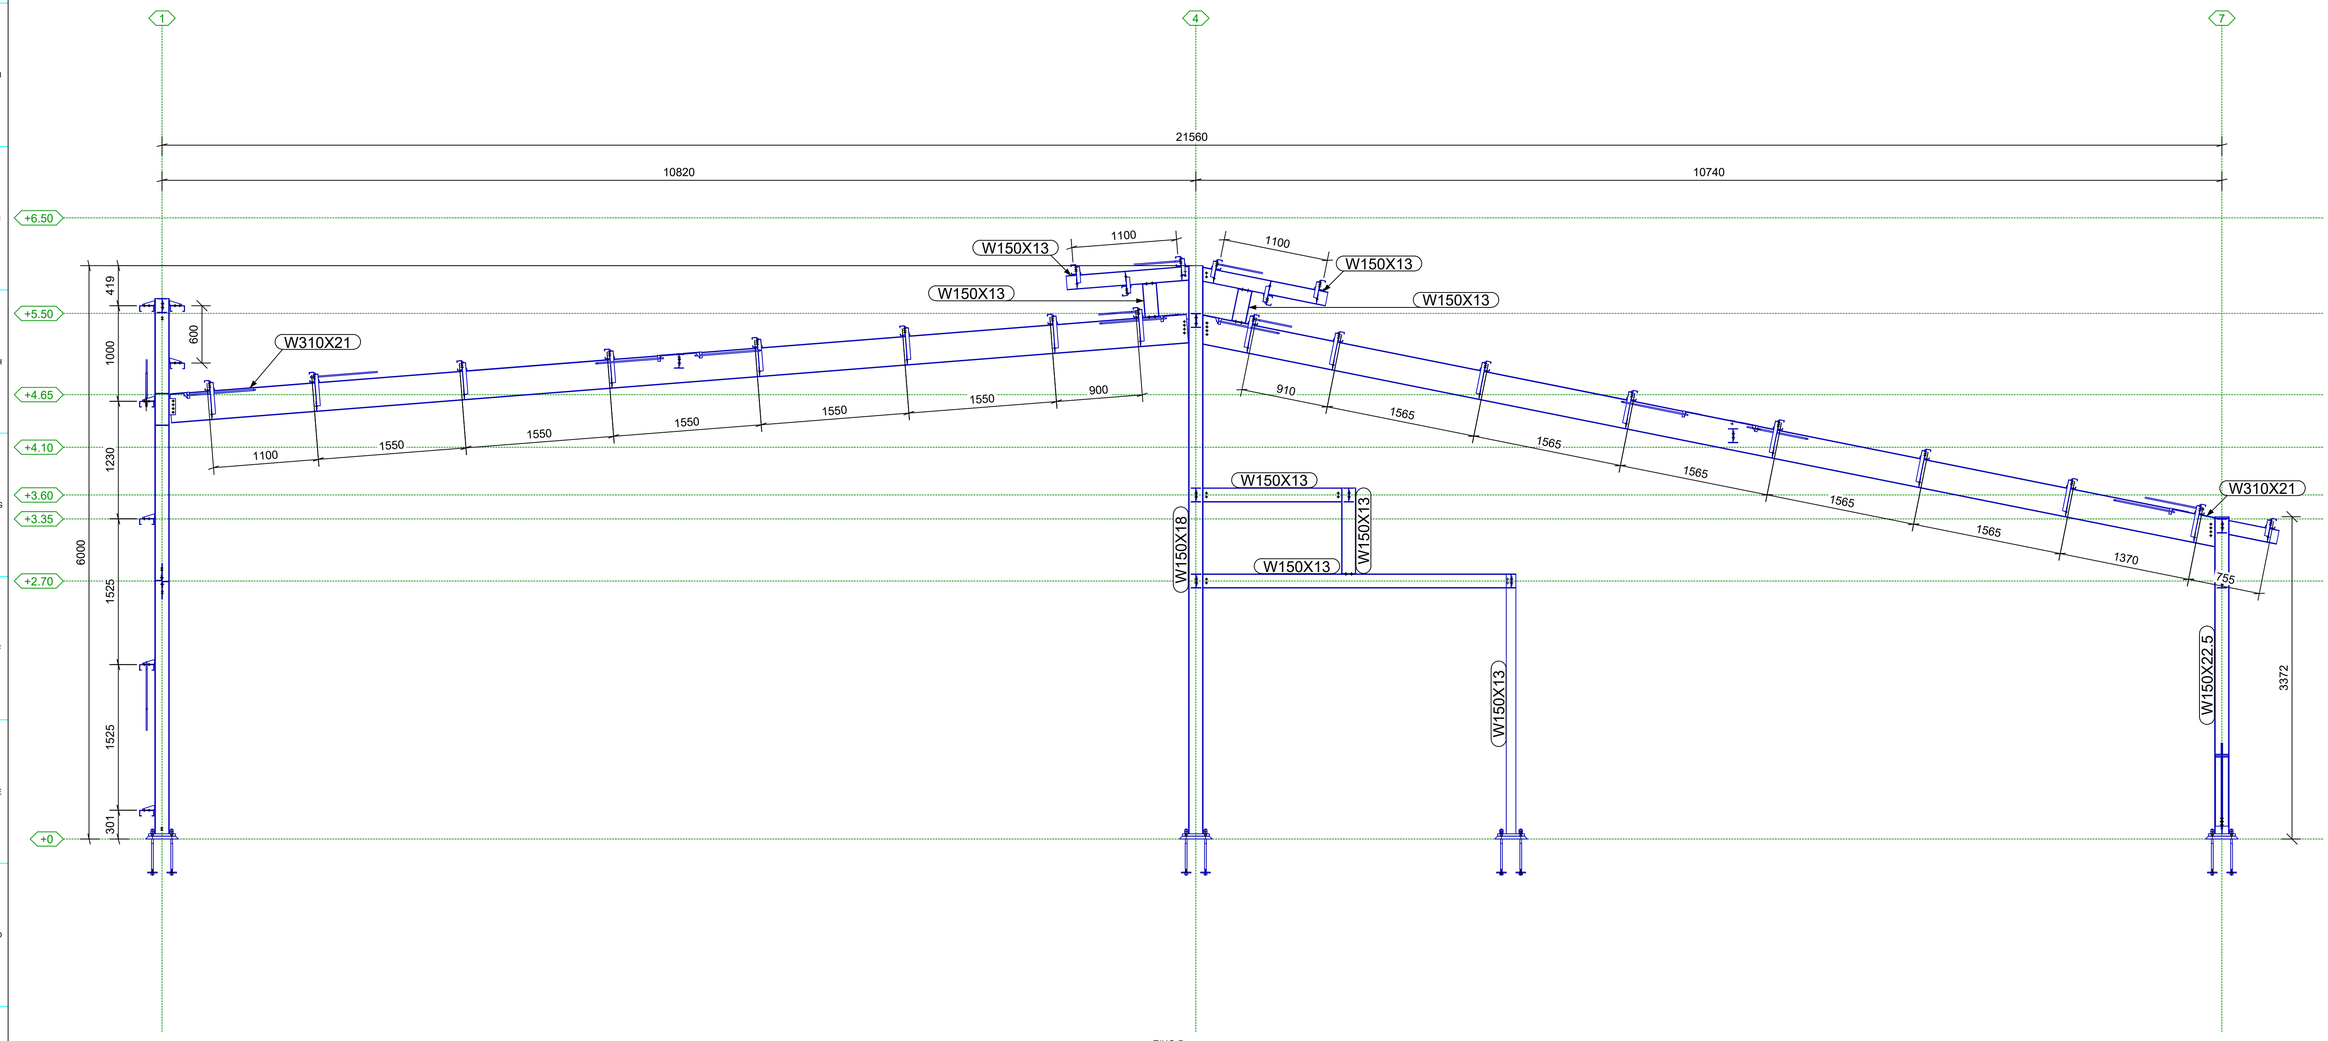

EIXO B
ESC.: 1:30

REV.	DATA	REVISOR	OBSERVAÇÕES
00	15/04/26	HELEN KÁSSIA	EMISSÃO INICIAL

STRUCKSTEEL

ESTRUTURAS METÁLICAS
strucksteelestruturasmetalicas@gmail.com

POSTO OPERACIONAL HIDROLÂNDIA

PROPRIETÁRIO:

PROJETISTA: CORPO DE BOMBEIROS MILITAR DE GOIÁS- CNPJ 33.638.099/0001-00

ENGº. JOÃO PEDRO GUIMARÃES BATISTELA - CREA 101.831.1009/D-GO


DESENHISTA:

ENGª. HELEN KÁSSIA PEREIRA SILVA - CREA 101.916.4573/D-GO


PROJETO ELABORADO SEGUINDO NORMAS VIGENTES - NBR8800:2024 (PERFIS LAMINADOS), NBR14762:2010 (PERFIS FORMADOS A FRIO), NBR6123:2023 (AÇÃO DO VENTO) E NBR8400:2019 (SOBRECARGA DE USO).

TÍTULO: EIXO B

FORMATO: A1	ARQUIVO: PA-2604-POH-01-R00		Nº PROJETO	REVISÃO
ESCALA: 1:30	DATA: 16/04/26	PÁGINA: 5	2604	00

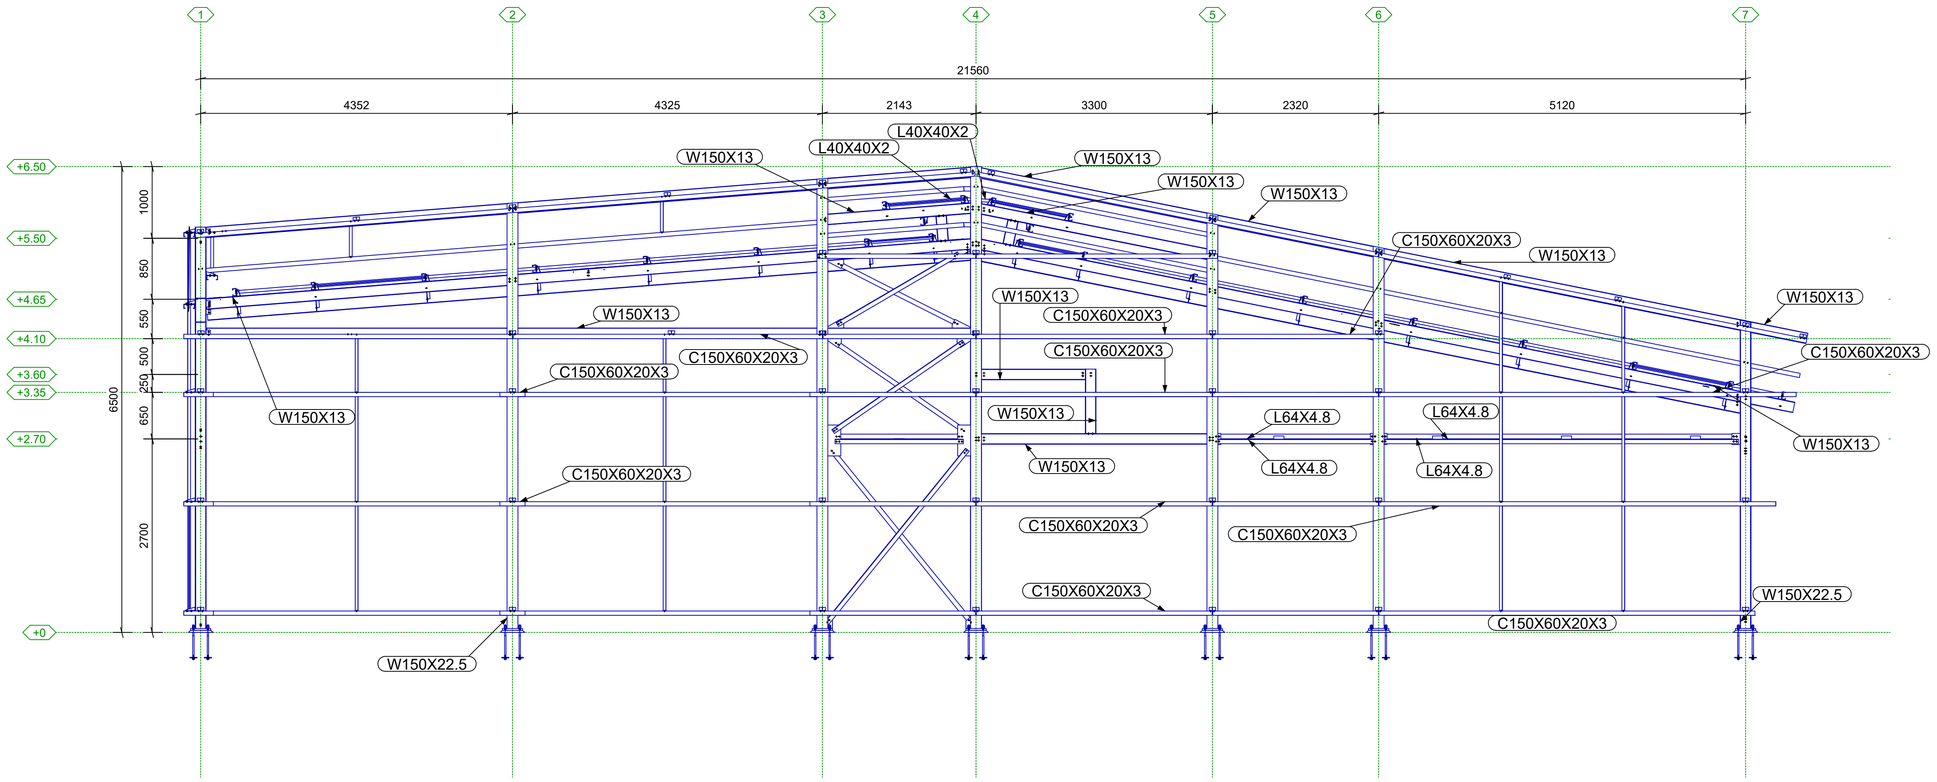

EIXO A
ESC.: 1:40

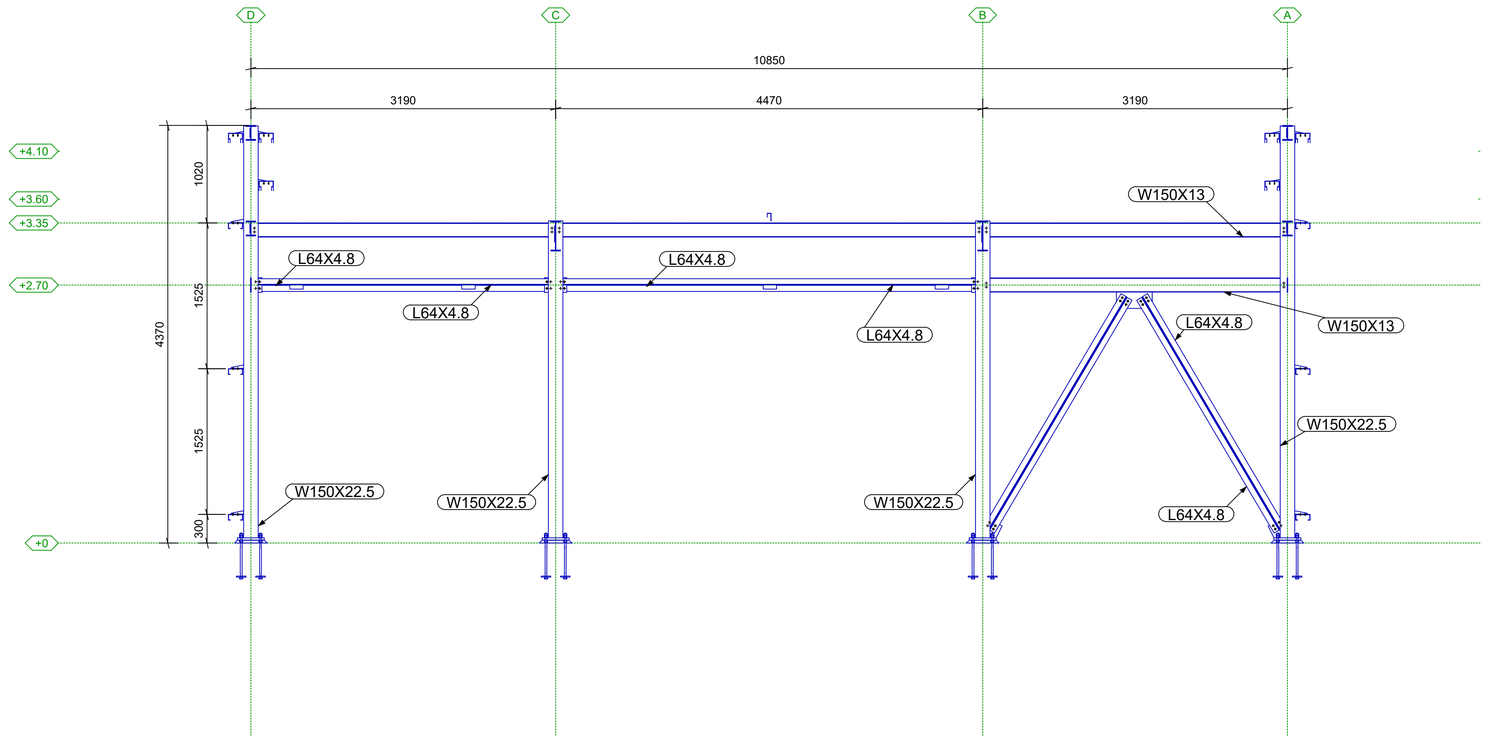

EIXO 6
ESC.: 1:30

REV.	DATA	REVISOR	OBSERVAÇÕES
00	15/04/26	HELEN KÁSSIA	EMISSÃO INICIAL

STRUCKSTEEL

ESTRUTURAS METÁLICAS
struckssteelestruturasmetalicas@gmail.com

POSTO OPERACIONAL HIDROLÂNDIA

PROPRIETÁRIO:

PROJETISTA: CORPO DE BOMBEIROS MILITAR DE GOIÁS- CNPJ 33.638.099/0001-00

ENGº. JOÃO PEDRO GUIMARÃES BATISTELA - CREA 101.831.1009/D-GO

DESENHISTA:

ENGª. HELEN KÁSSIA PEREIRA SILVA - CREA 101.916.4573/D-GO


PROJETO ELABORADO SEGUINDO NORMAS VIGENTES - NBR8800:2024 (PERFIS LAMINADOS), NBR14762:2010 (PERFIS FORMADOS A FRIO), NBR6123:2023 (AÇÃO DO VENTO) E NBR8120:2016 (SOBRECARGA DE USO).

TÍTULO: EIXO A
EIXO 6


FORMATO: A1	ARQUIVO: PA-2604-POH-01-R00		Nº PROJETO	REVISÃO
ESCALA: 1:30	DATA: 16/04/26	PÁGINA: 6	2604	00

ESTE DOCUMENTO NÃO PODE SER REPRODUZIDO, INTEGRAL OU PARCIALMENTE, POR QUALQUER MEIO, INCLUINDO FOTOCÓPIA, SEM AUTORIZAÇÃO

ESTE DOCUMENTO NÃO PODE SER REPRODUZIDO, INTEGRAL OU PARCIALMENTE, POR QUALQUER MEIO, INCLUINDO FOTOCÓPIA, SEM AUTORIZAÇÃO

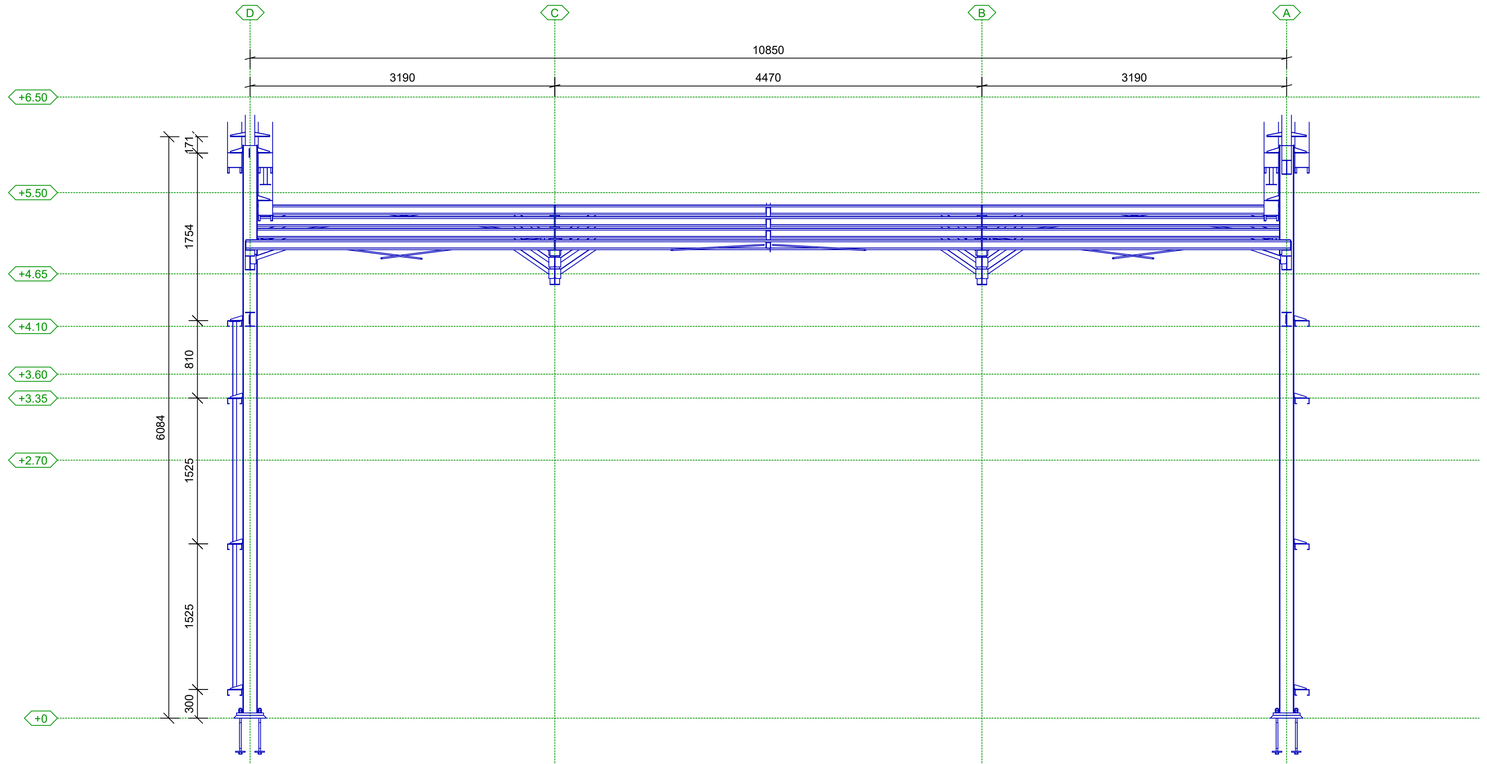

EIXO 2
ESC.: 1:30

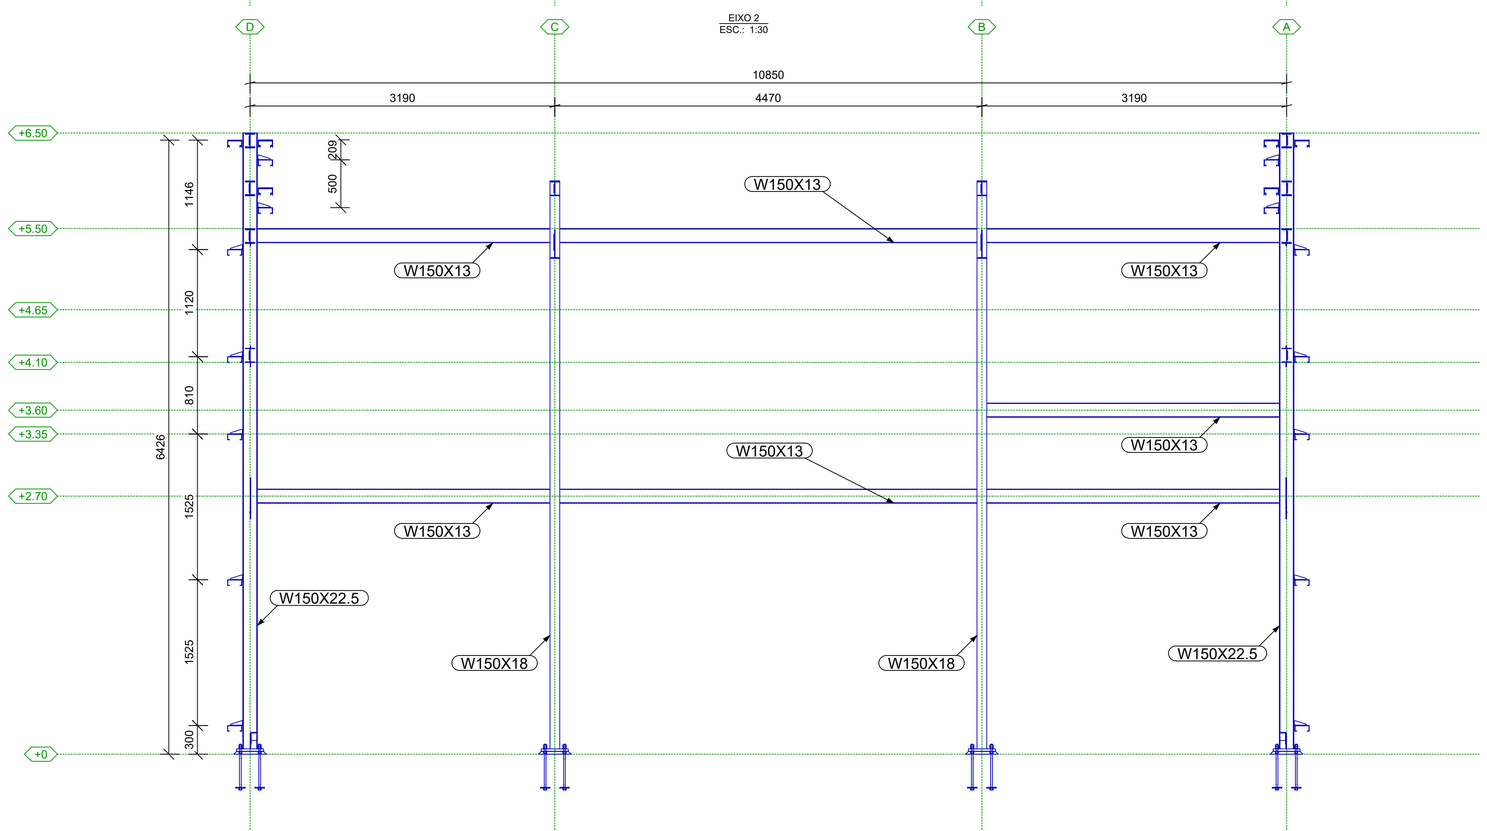

EIXO 3
ESC.: 1:30

REV.	DATA	REVISOR	OBSERVAÇÕES
00	15/04/26	HELEN KÁSSIA	EMISSÃO INICIAL

STRUCKSTEEL

ESTRUTURAS METÁLICAS
strucksteelestruturasmetalicas@gmail.com

POSTO OPERACIONAL HIDROLÂNDIA

PROPRIETÁRIO:

PROJETISTA: CORPO DE BOMBEIROS MILITAR DE GOIÁS- CNPJ 33.638.099/0001-00

ENGº. JOÃO PEDRO GUIMARÃES BATISTELA - CREA 101.831.1009/D-GO

DESENHISTA:

ENGª. HELEN KÁSSIA PEREIRA SILVA - CREA 101.916.4573/D-GO

PROJETO ELABORADO SEGUINDO NORMAS VIGENTES - NBR8800:2024 (PERFIS LAMINADOS), NBR14762:2010 (PERFIS FORMADOS A FRIO), NBR6123:2023 (AÇÃO DO VENTO) E NBR8400:2019 (SOBRECARGA DE USO).

TÍTULO: EIXO 3
EIXO 2

FORMATO: A1	ARQUIVO: PA-2604-POH-01-R00		Nº PROJETO	REVISÃO
ESCALA: 1:30	DATA: 16/04/26	PÁGINA: 7	2604	00