

ESTE DOCUMENTO NÃO PODE SER REPRODUZIDO, INTEIRA OU PARCIALMENTE, POR QUALQUER MEIO, INCLUINDO FOTOCÓPIA, SEM AUTORIZAÇÃO


LISTA DE RESUMO DE MATERIAL

PERFIL	MATERIAL	QTD(mm/m²)	PESO (Kg)	SUP. (m²)
3/4"Ø_HEAVY_HEX_NUT	A36	4560	24.0	1.1
3/4"Ø_WASHER	A36	240	0.0	0.1
BARRA RED.19	A36	28860	66.0	1.7
C127X50X17X2.65	CIVIL 300	300000	1157.4	151.9
C150X60X20X2.65	CIVIL 300	11880	72.2	7.2
C200X75X17X2	CIVIL 300	122208	723.1	92.4
C200X75X25X2.65	CIVIL 300	431027	3342.1	335.9
CALHA U 400	ALUMINIO	49640	39.6	41.5
PL10X100	A36	1	48.0	1.4
TELHA TP40	TELHA	351000	1679.6	0.0
U154X50X2	CIVIL 300	17806	135.7	8.1
CH. 25.0	A36	1.65	324.0	3.8
PESO TOTAL: 7611.7 Kg		SUPERFICIE A TRATAR: 645.2 m²		

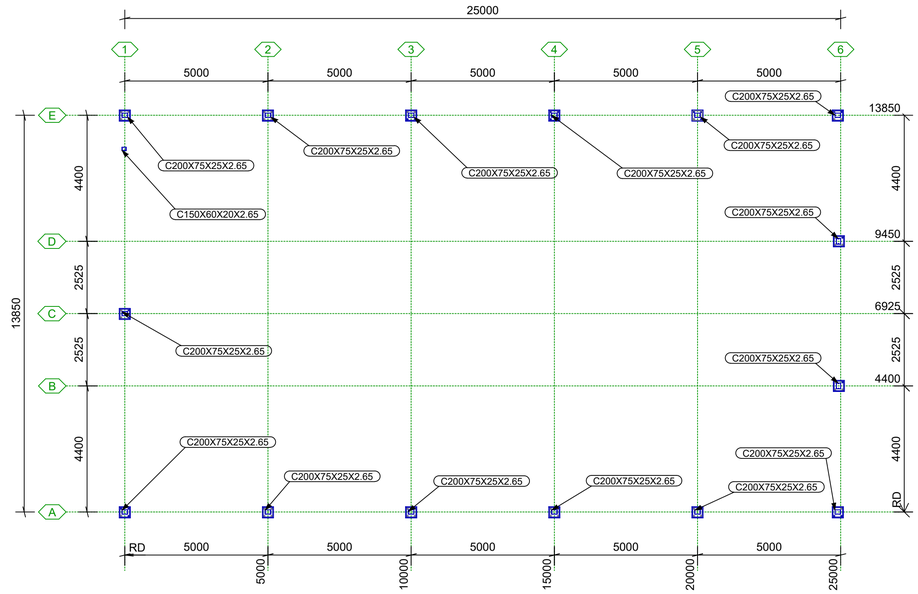


PLANTA DE LOCAÇÃO
ESC.: 1:100

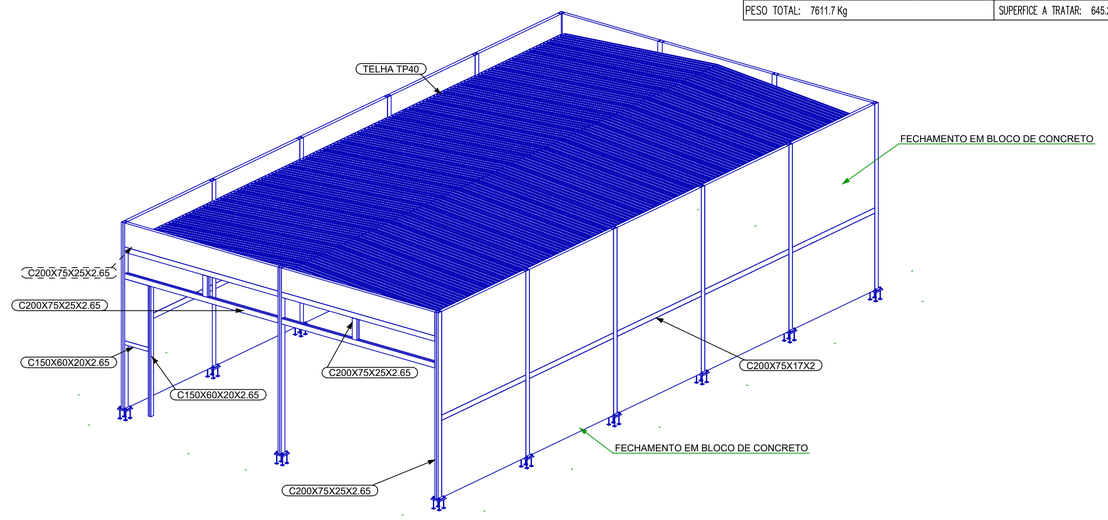


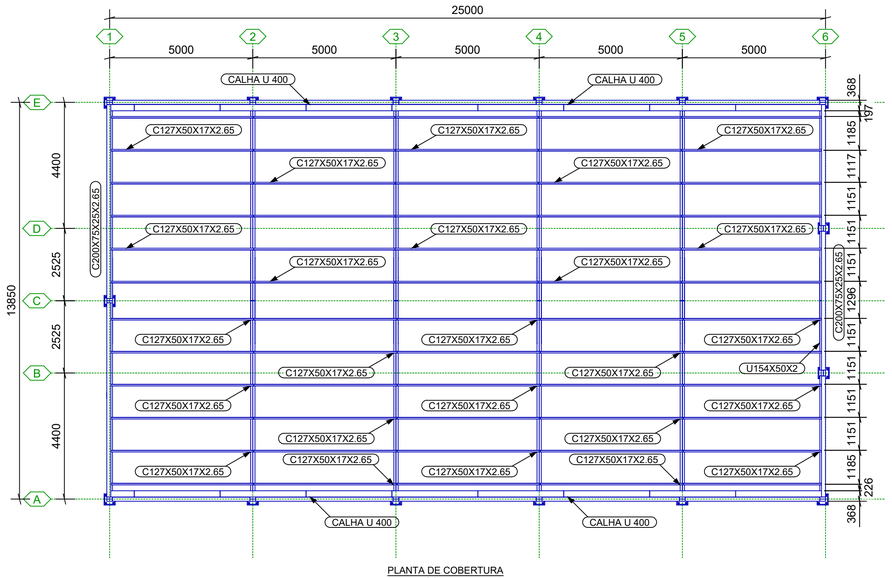

PLANTA DE COBERTURA
ESC.: 1:100

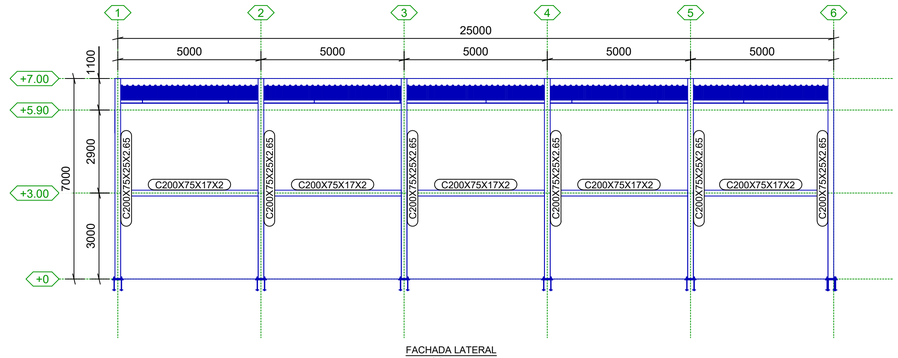

FACHADA LATERAL
ESC.: 1:100

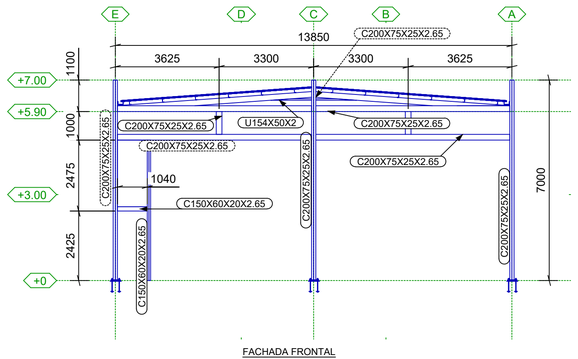

FACHADA FRONTAL
ESC.: 1:100

00	20/04/26	HELEN KÁSSIA	EMISSÃO INICIAL
REV.	DATA	REVISOR	OBSERVAÇÕES

STRUCKSTEEL

ESTRUTURAS METÁLICAS
struckssteelestruturasmetalicas@gmail.com

GALPAO GOLD PAULO

PROPRIETÁRIO:

PROJETISTA: GOLD PARTICIPAÇÕES - CNPJ 25.037.422/0001-62

DESENHISTA: ENGº. JOÃO PEDRO GUIMARÃES BATISTELA - CREA 101.831.1009/D-GO

ENGº. HELEN KÁSSIA PEREIRA SILVA - CREA 101.916.4573/D-GO

PROJETO ELABORADO SEGUINDO NORMAS VIGENTES - NBR8800:2024 (PERFIS LAMINADOS), NBR14762:2010 (PERFIS FORMADOS A FRIO), NBR6123:2023 (AÇÃO DO VENTO) E NBR6120:2019 (SOBRECARGA DE USO).

TÍTULO: PLANTA DE LOCAÇÃO
PLANTA DE COBERTURA
FACHADAS
PERSPECTIVA

FORMATO: A1	ARQUIVO: PA -2605-GGP-01-R00	Nº PROJETO	REVISÃO
ESCALA: 1:100	DATA: 20/04/26	PÁGINA: 1	2605 — 00