
ESTE DOCUMENTO NÃO PODE SER REPRODUZIDO, INTEGRAL OU PARCIALMENTE, POR QUALQUER MEIO, INCLUINDO FOTOCÓPIA, SEM AUTORIZAÇÃO

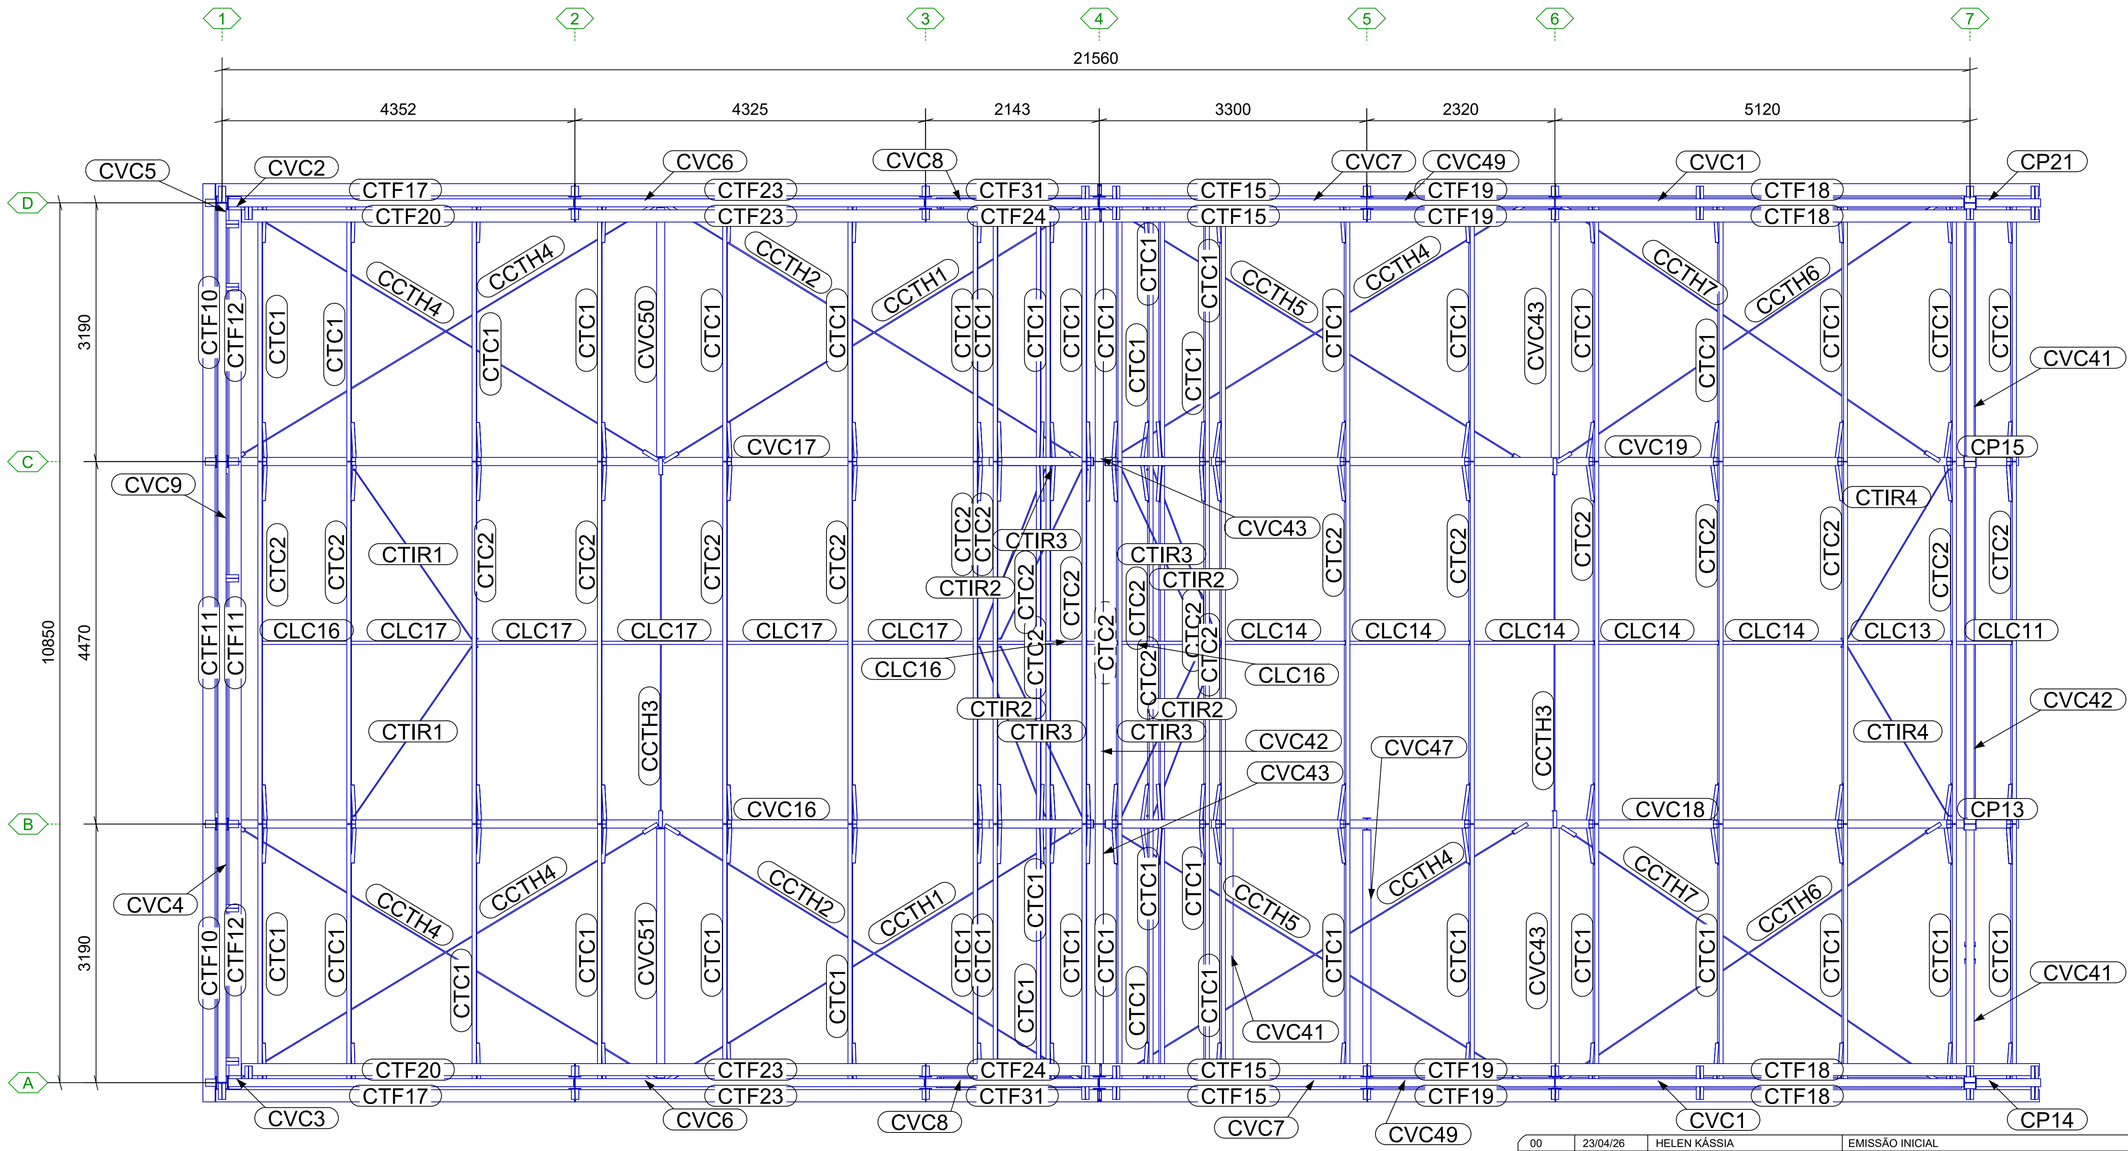

PLANTA DE COBERTURA

ESC.: 1:50

REV.	DATA	REVISOR	OBSERVAÇÕES
00	23/04/26	HELEN KÁSSIA	EMISSÃO INICIAL

STRUCKSTEEL
ESTRUTURAS METÁLICAS
struckssteelestruturasmetalicas@gmail.com

POSTO OPERACIONAL HIDROLÂNDIA

PROPRIETÁRIO:

PROJETISTA: CORPO DE BOMBEIROS MILITAR DE GOIÁS- CNPJ 33.638.099/0001-00

DESENHISTA: ENGº. JOÃO PEDRO GUIMARÃES BATISTELA - CREA 101.831.1009/D-GO

ENGª. HELEN KÁSSIA PEREIRA SILVA - CREA 101.916.4573/D-GO


PROJETO ELABORADO SEGUNDO NORMAS VIGENTES - NBR8800:2024 (PERFIS LAMINADOS), NBR14762:2010 (PERFIS FORMADOS A FRIO), NBR6123:2023 (AÇÃO DO VENTO) E NBR6120:2019 (SOBRECARGA DE USO).

TÍTULO: PLANTA DE COBERTURA

FORMATO: A1	ARQUIVO: PM-2604-POH-01-R00		Nº PROJETO	REVISÃO
ESCALA: 1:50	DATA: 23/04/26	PÁGINA: 1	2604	00

Tekla Structures

ESTE DOCUMENTO NÃO PODE SER REPRODUZIDO, INTEGRAL OU PARCIALMENTE, POR QUALQUER MEIO, INCLUINDO FOTOCOPIA, SEM AUTORIZAÇÃO

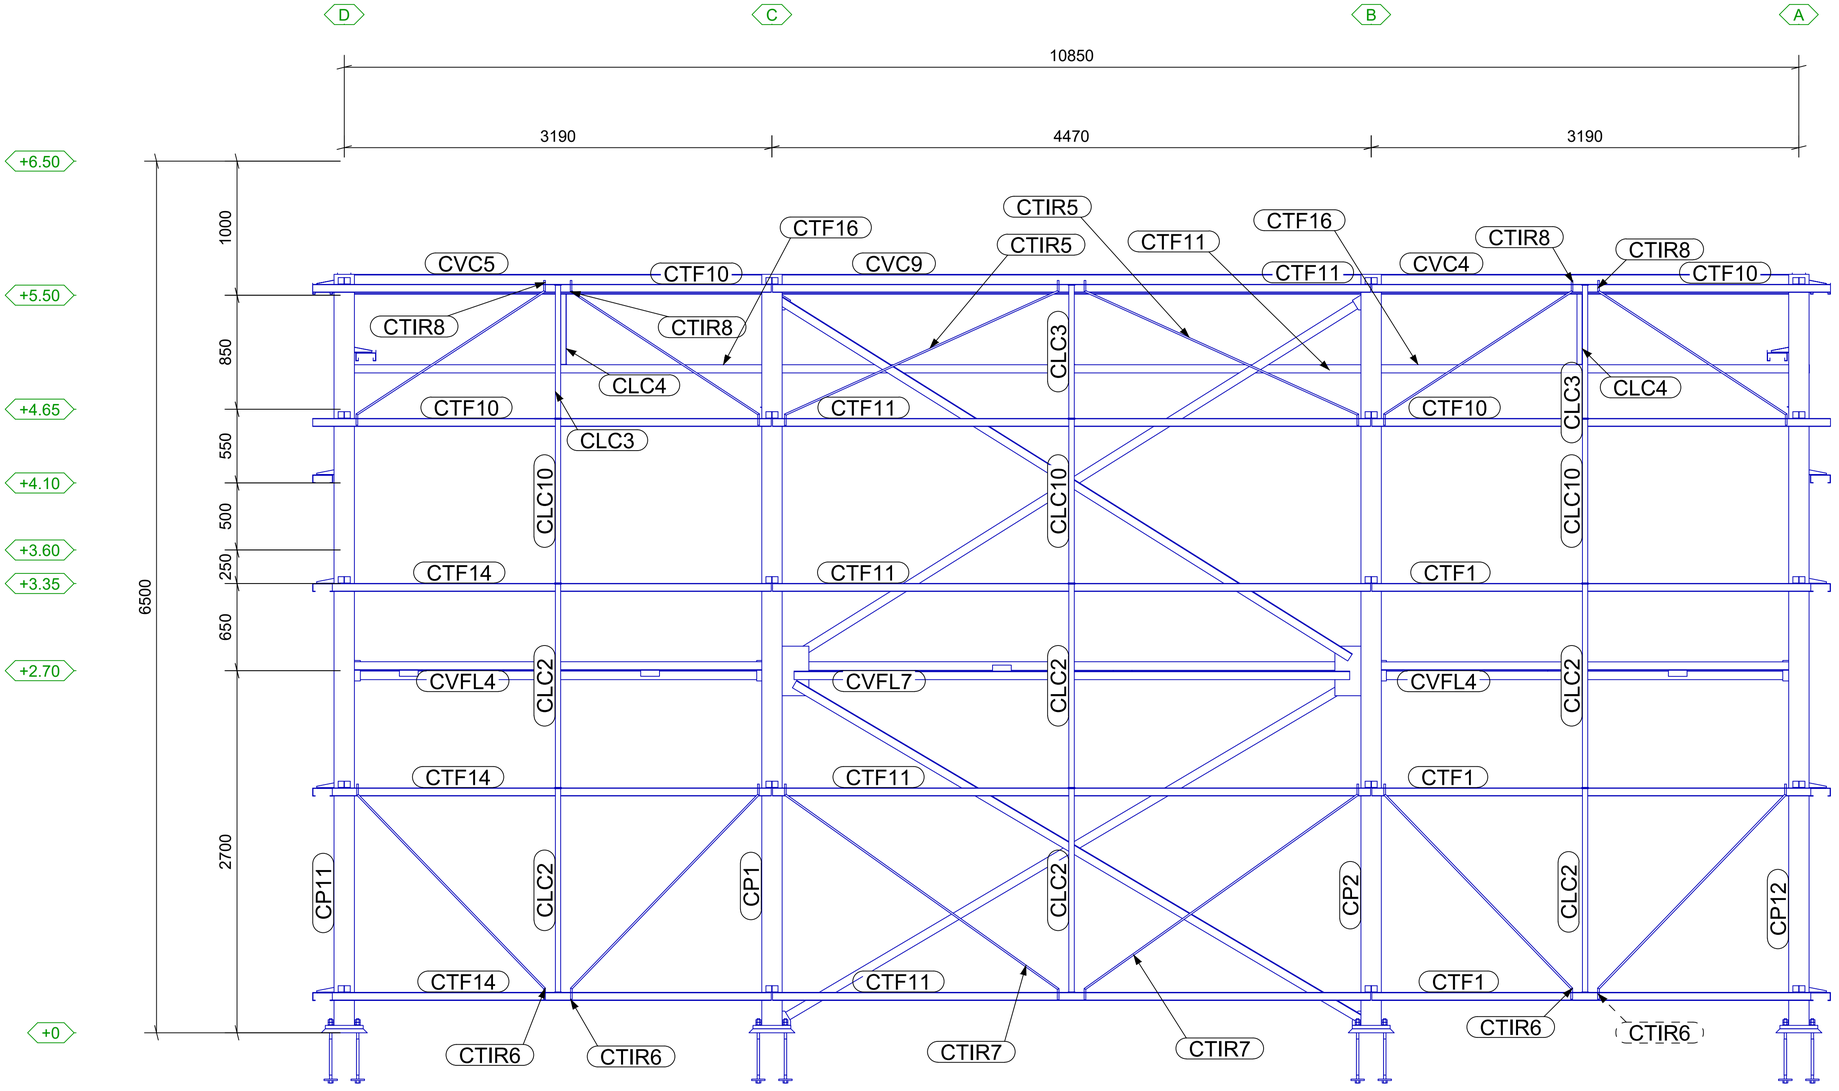

EIXO 1
ESC.: 1:30

REV.	DATA	REVISOR	OBSERVAÇÕES
00	23/04/26	HELEN KÁSSIA	EMISSÃO INICIAL

STRUCKSTEEL
ESTRUTURAS METÁLICAS
strucksteelestruturasmetalicas@gmail.com

POSTO OPERACIONAL HIDROLÂNDIA

PROPRIETÁRIO:

PROJETISTA: CORPO DE BOMBEIROS MILITAR DE GOIÁS- CNPJ 33.638.099/0001-00

DESENHISTA: ENGº. JOÃO PEDRO GUIMARÃES BATISTELA - CREA 101.831.1009/D-GO


ENGª. HELEN KÁSSIA PEREIRA SILVA - CREA 101.916.4573/D-GO

PROJETO ELABORADO SEGUINDO NORMAS VIGENTES - NBR8800:2024 (PERFIS LAMINADOS), NBR14762:2010 (PERFIS FORMADOS A FRIO), NBR6123:2023 (AÇÃO DO VENTO) E NBR6120:2019 (SOBRECARGA DE USO).

TÍTULO: EIXO 1

FORMATO: A1	ARQUIVO: PM-2604-POH-01-R00		Nº PROJETO	REVISÃO
ESCALA: 1:30	DATA: 23/04/26	PÁGINA: 1	2604	00

Tekla Structures

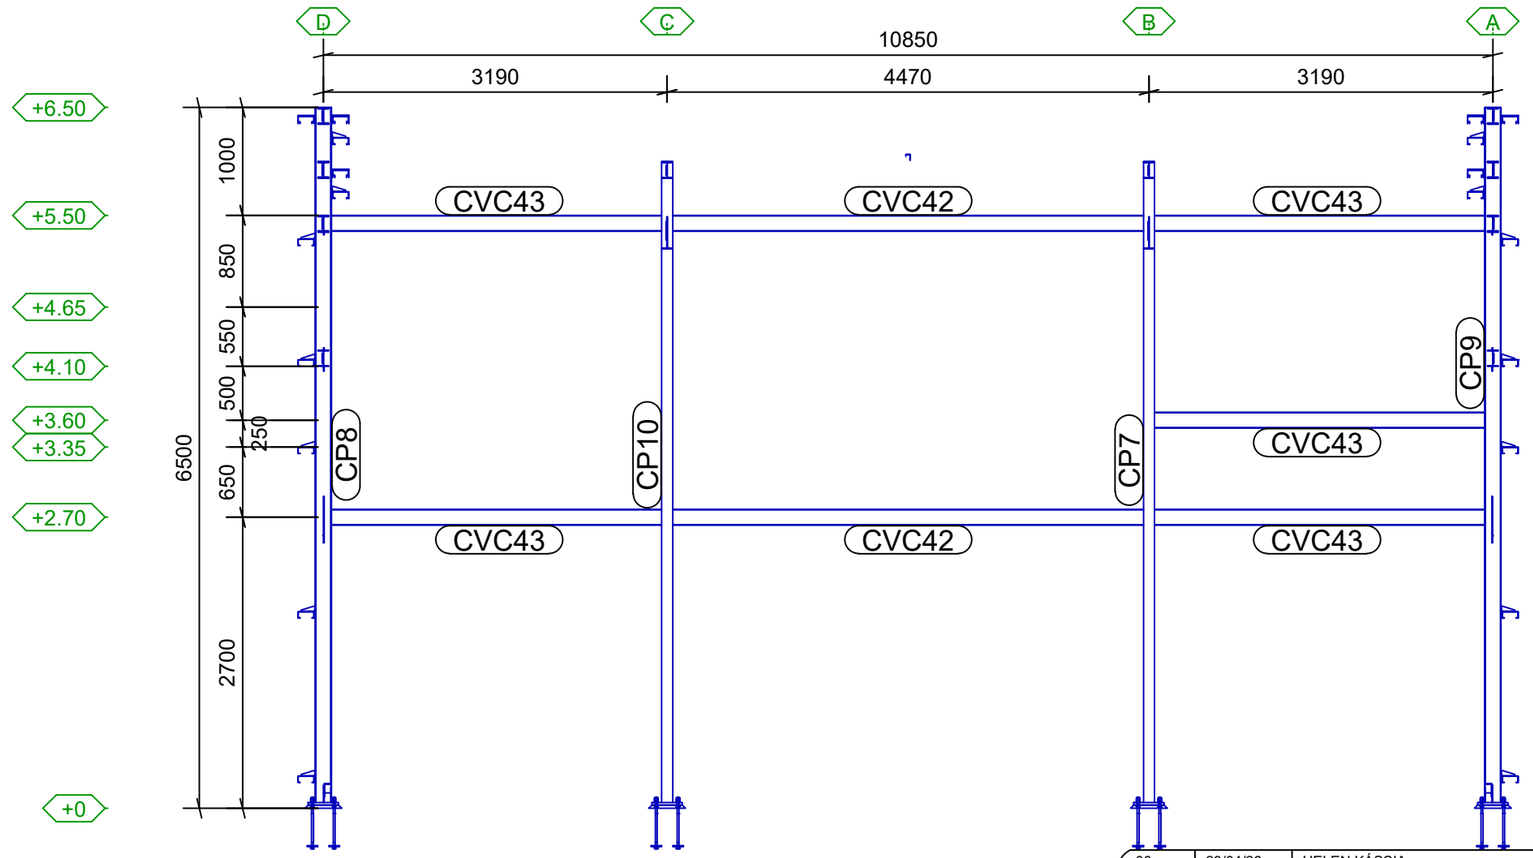

EIXO 3
ESC.: 1:50

REV.	DATA	REVISOR	OBSERVAÇÕES
00	23/04/26	HELEN KÁSSIA	EMISSÃO INICIAL

STRUCKSTEEL

ESTRUTURAS METÁLICAS
strucksteelestruturasmetalicas@gmail.com

POSTO OPERACIONAL HIDROLÂNDIA

PROPRIETÁRIO:

PROJETISTA: CORPO DE BOMBEIROS MILITAR DE GOIÁS- CNPJ 33.638.099/0001-00

DESENHISTA: ENGº. JOÃO PEDRO GUIMARÃES BATISTELA - CREA 101.831.1009/D-GO

ENGª. HELEN KÁSSIA PEREIRA SILVA - CREA 101.916.4573/D-GO


PROJETO ELABORADO SEGUNDO NORMAS VIGENTES - NBR8800:2024 (PERFIS LAMINADOS), NBR14762:2010 (PERFIS FORMADOS A FRIO), NBR6123:2023 (AÇÃO DO VENTO) E NBR6120:2019 (SOBRECARGA DE USO).

TÍTULO: EIXO 3

FORMATO: A1	ARQUIVO: PM-2604-POH-01-R00		Nº PROJETO	REVISÃO
ESCALA: 1:50	DATA: 23/04/26	PÁGINA: 1	2604	00

ESTE DOCUMENTO NÃO PODE SER REPRODUZIDO, INTEGRAL OU PARCIALMENTE, POR QUALQUER MEIO, INCLUINDO FOTOCOPIA, SEM AUTORIZAÇÃO

Tekla Structures

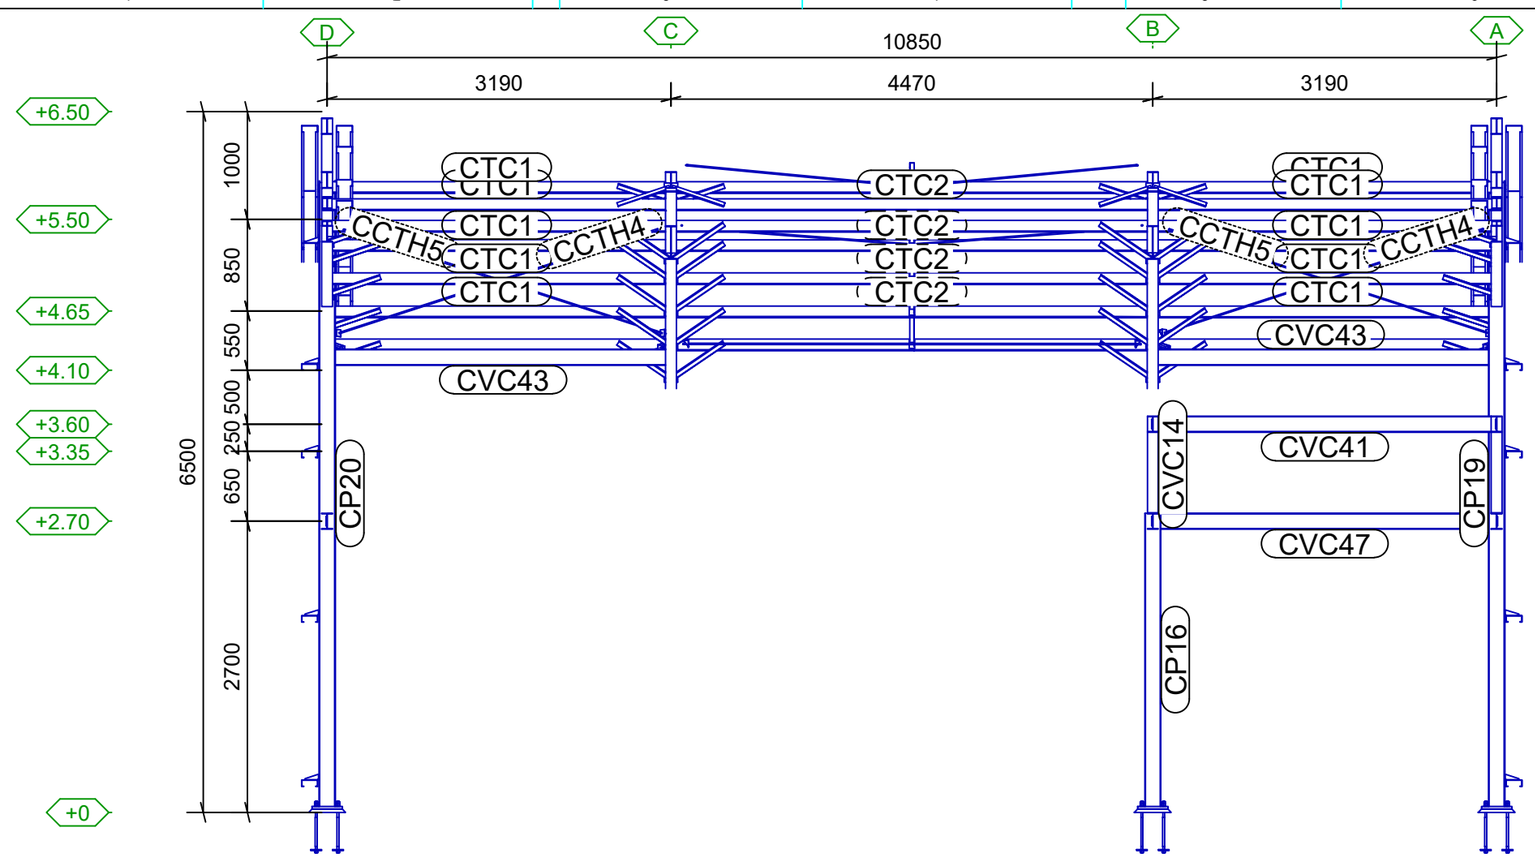

EIXO 4
ESC.: 1:50

REV.	DATA	REVISOR	OBSERVAÇÕES
00	23/04/26	HELEN KÁSSIA	EMISSÃO INICIAL

STRUCKSTEEL

ESTRUTURAS METÁLICAS
strucksteelestruturasmetalicas@gmail.com

POSTO OPERACIONAL HIDROLÂNDIA

PROPRIETÁRIO:

PROJETISTA: CORPO DE BOMBEIROS MILITAR DE GOIÁS- CNPJ 33.638.099/0001-00

DESENHISTA: ENGº. JOÃO PEDRO GUIMARÃES BATISTELA - CREA 101.831.1009/D-GO

ENGª. HELEN KÁSSIA PEREIRA SILVA - CREA 101.916.4573/D-GO

PROJETO ELABORADO SEGUNDO NORMAS VIGENTES - NBR8800:2024 (PERFIS LAMINADOS), NBR14762:2010 (PERFIS FORMADOS A FRIO), NBR6123:2023 (AÇÃO DO VENTO) E NBR6120:2019 (SOBRECARGA DE USO).


TÍTULO: EIXO 4

FORMATO: A1	ARQUIVO: PM-2604-POH-01-R00		Nº PROJETO	REVISÃO
ESCALA: 1:50	DATA: 23/04/26	PÁGINA: 1	2604	00

ESTE DOCUMENTO NÃO PODE SER REPRODUZIDO, INTEGRAL OU PARCIALMENTE, POR QUALQUER MEIO, INCLUINDO FOTOCOPIA, SEM AUTORIZAÇÃO

Tekla Structures

ESTE DOCUMENTO NÃO PODE SER REPRODUZIDO, INTEGRAL OU PARCIALMENTE, POR QUALQUER MEIO, INCLUINDO FOTOCÓPIA, SEM AUTORIZAÇÃO

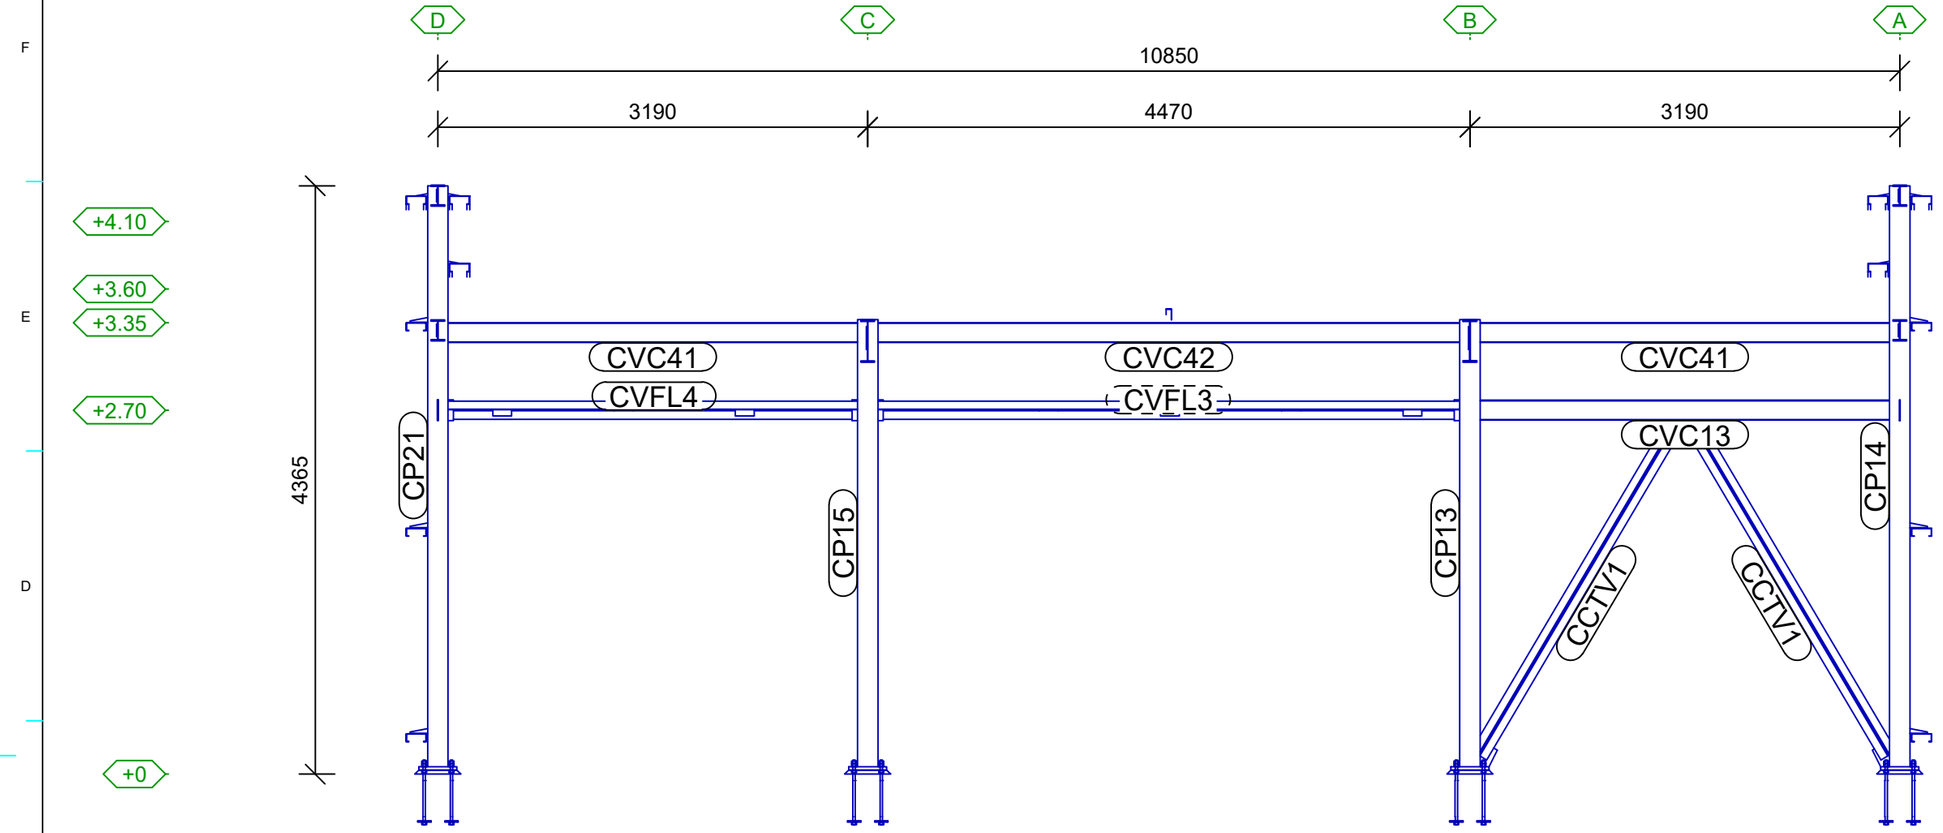

EIXO 6
ESC.: 1:40

REV.	DATA	REVISOR	OBSERVAÇÕES
00	23/04/26	HELEN KÁSSIA	EMISSÃO INICIAL

STRUCKSTEEL
ESTRUTURAS METÁLICAS
strucksteelestruturasmetalicas@gmail.com

POSTO OPERACIONAL HIDROLÂNDIA

PROPRIETÁRIO: CORPO DE BOMBEIROS MILITAR DE GOIÁS- CNPJ 33.638.099/0001-00

PROJETISTA: ENGº. JOÃO PEDRO GUIMARÃES BATISTELA - CREA 101.831.1009/D-GO

DESENHISTA: ENGª. HELEN KÁSSIA PEREIRA SILVA - CREA 101.916.4573/D-GO


PROJETO ELABORADO SEGUNDO NORMAS VIGENTES - NBR8800:2024 (PERFIS LAMINADOS), NBR14762:2010 (PERFIS FORMADOS A FRIO), NBR6123:2023 (AÇÃO DO VENTO) E NBR6120:2019 (SOBRECARGA DE USO).

TÍTULO: EIXO 6

FORMATO: A1	ARQUIVO: PM-2604-POH-01-R00		Nº PROJETO: 2604
ESCALA: 1:40	DATA: 23/04/26	PÁGINA: 1	REVISÃO: 00

Tekla Structures

ESTE DOCUMENTO NÃO PODE SER REPRODUZIDO, INTEGRAL OU PARCIALMENTE, POR QUALQUER MEIO, INCLUINDO FOTOCÓPIA, SEM AUTORIZAÇÃO

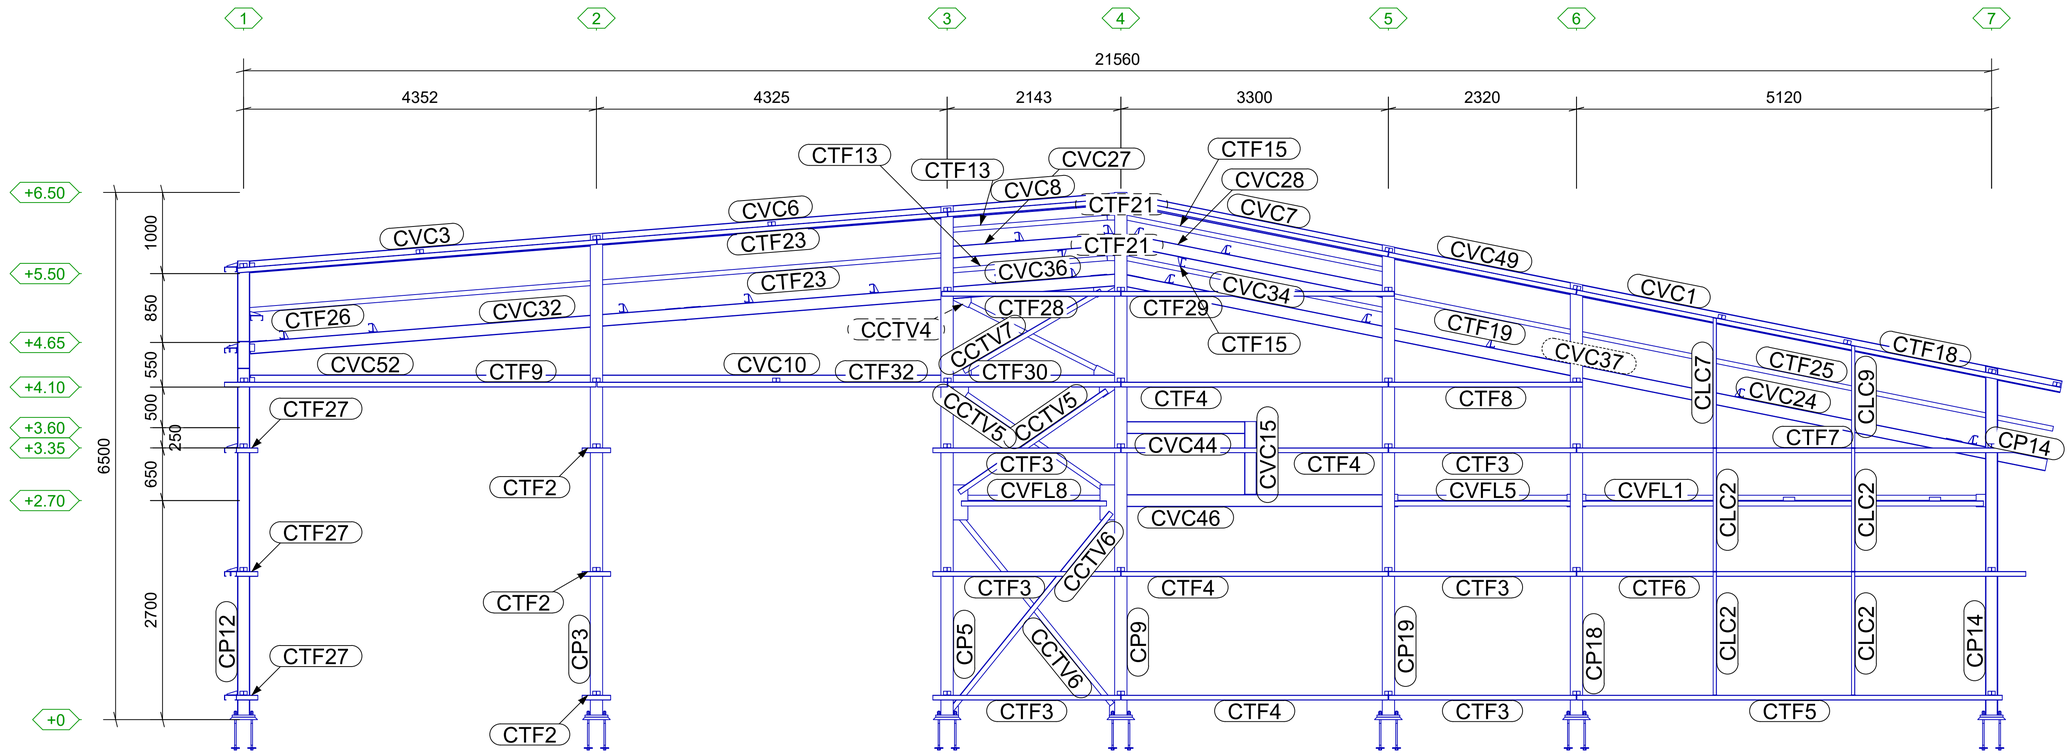

EIXO A
ESC.: 1:50

REV.	DATA	REVISOR	OBSERVAÇÕES
00	23/04/26	HELEN KÁSSIA	EMISSÃO INICIAL

ESTRUTURAS METÁLICAS
struckssteelestruturasmetalicas@gmail.com

POSTO OPERACIONAL HIDROLÂNDIA

PROPRIETÁRIO:

PROJETISTA: CORPO DE BOMBEIROS MILITAR DE GOIÁS- CNPJ 33.638.099/0001-00

DESENHISTA: ENGº. JOÃO PEDRO GUIMARÃES BATISTELA - CREA 101.831.1009/D-GO

ENGª. HELEN KÁSSIA PEREIRA SILVA - CREA 101.916.4573/D-GO


PROJETO ELABORADO SEGUNDO NORMAS VIGENTES - NBR8800:2024 (PERFIS LAMINADOS), NBR14762:2010 (PERFIS FORMADOS A FRIO), NBR6123:2023 (AÇÃO DO VENTO) E NBR6120:2019 (SOBRECARGA DE USO).

TÍTULO: EIXO A

FORMATO: A1	ARQUIVO: PM-2604-POH-01-R00		Nº PROJETO	REVISÃO
ESCALA: 1:50	DATA: 23/04/26	PÁGINA: 1	2604	00

Tekla Structures

ESTE DOCUMENTO NÃO PODE SER REPRODUZIDO, INTEGRAL OU PARCIALMENTE, POR QUALQUER MEIO, INCLUINDO FOTOCÓPIA, SEM AUTORIZAÇÃO

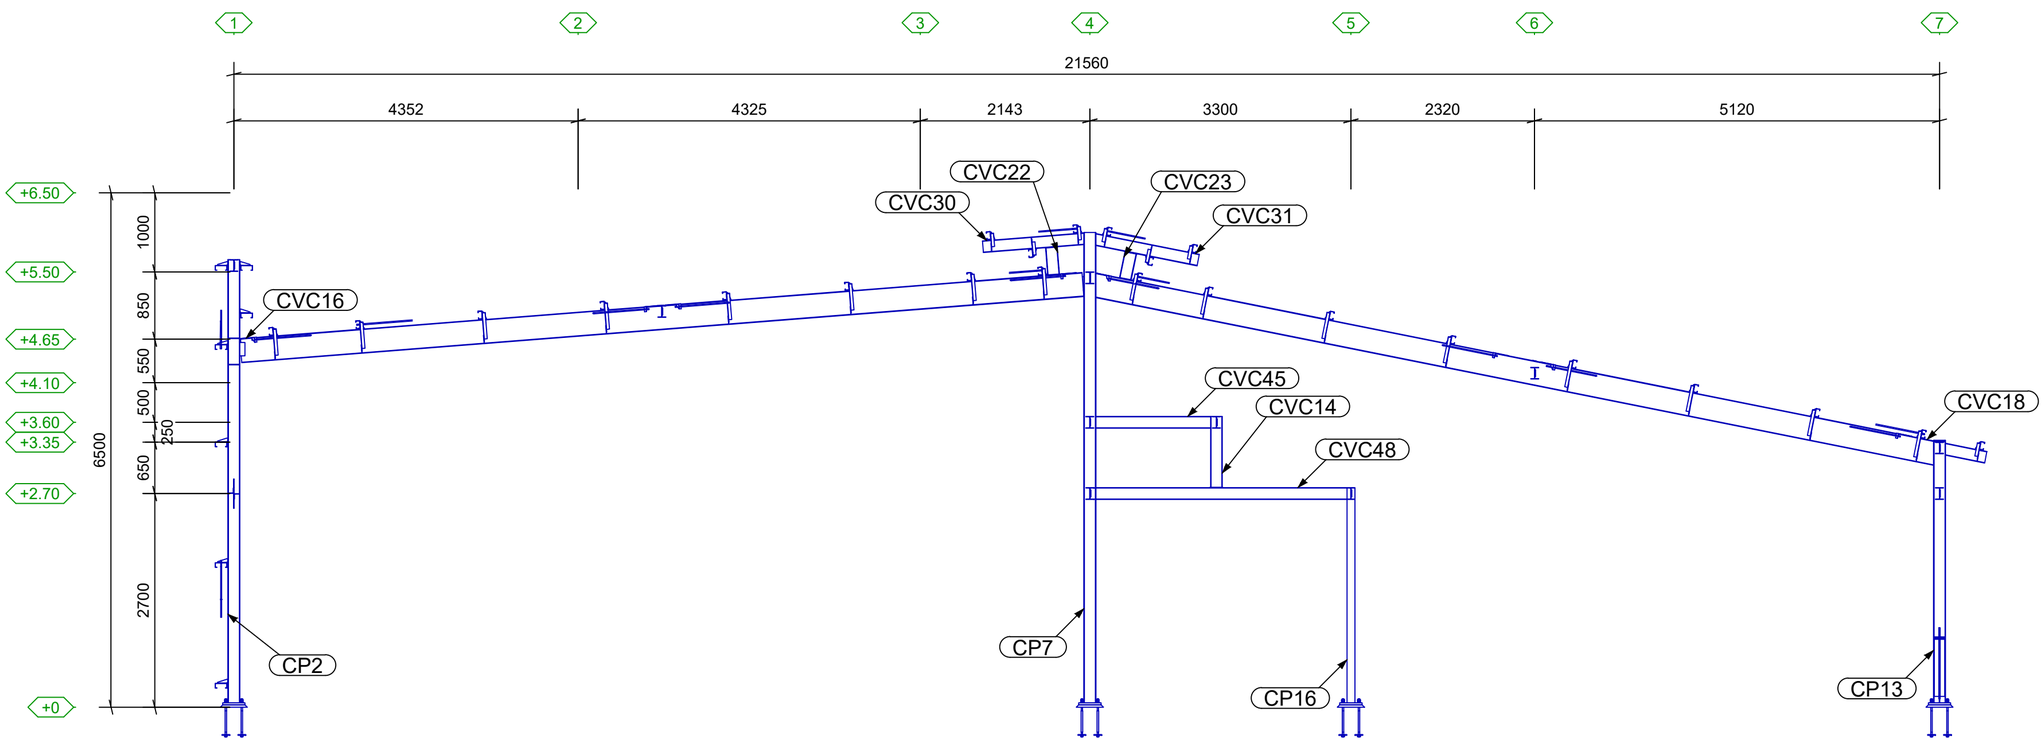

EIXO B
ESC.: 1:50

REV.	DATA	REVISOR	OBSERVAÇÕES
00	23/04/26	HELEN KÁSSIA	EMISSÃO INICIAL

STRUCKSTEEL

ESTRUTURAS METÁLICAS
strucksteelestruturasmetalicas@gmail.com

POSTO OPERACIONAL HIDROLÂNDIA

PROPRIETÁRIO:

PROJETISTA: CORPO DE BOMBEIROS MILITAR DE GOIÁS- CNPJ 33.638.099/0001-00

DESENHISTA: ENGº. JOÃO PEDRO GUIMARÃES BATISTELA - CREA 101.831.1009/D-GO

ENGª. HELEN KÁSSIA PEREIRA SILVA - CREA 101.916.4573/D-GO


PROJETO ELABORADO SEGUNDO NORMAS VIGENTES - NBR8800:2024 (PERFIS LAMINADOS), NBR14762:2010 (PERFIS FORMADOS A FRIO), NBR6123:2023 (AÇÃO DO VENTO) E NBR6120:2019 (SOBRECARGA DE USO).

TÍTULO: EIXO B

FORMATO: A1	ARQUIVO: PM-2604-POH-01-R00		Nº PROJETO	REVISÃO
ESCALA: 1:50	DATA: 23/04/26	PÁGINA: 1	2604	00

Tekla Structures

ESTE DOCUMENTO NÃO PODE SER REPRODUZIDO, INTEGRAL OU PARCIALMENTE, POR QUALQUER MEIO, INCLUINDO FOTOCÓPIA, SEM AUTORIZAÇÃO

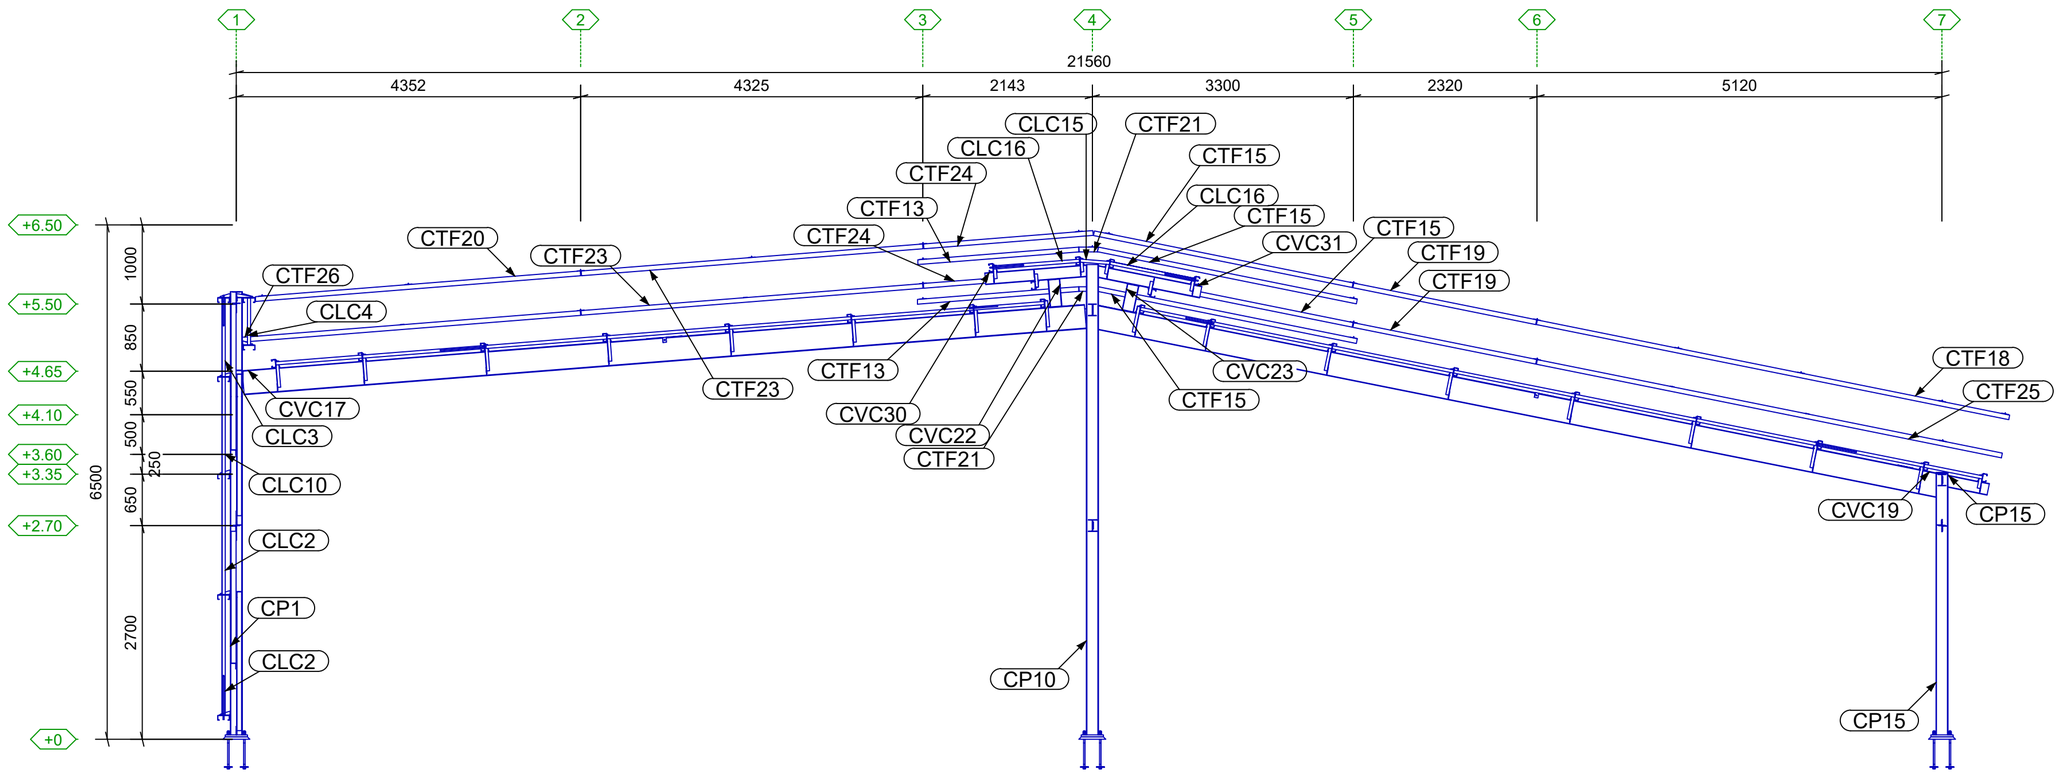

EIXO D
ESC.: 1:50

REV.	DATA	REVISOR	OBSERVAÇÕES
00	23/04/26	HELEN KÁSSIA	EMISSÃO INICIAL

ESTRUTURAS METÁLICAS
strucksteelestruturasmetalicas@gmail.com

POSTO OPERACIONAL HIDROLÂNDIA

PROPRIETÁRIO: CORPO DE BOMBEIROS MILITAR DE GOIÁS- CNPJ 33.638.099/0001-00

PROJETISTA: ENGº. JOÃO PEDRO GUIMARÃES BATISTELA - CREA 101.831.1009/D-GO

DESENHISTA: ENGª. HELEN KÁSSIA PEREIRA SILVA - CREA 101.916.4573/D-GO


PROJETO ELABORADO SEGUNDO NORMAS VIGENTES - NBR8800:2024 (PERFIS LAMINADOS), NBR14762:2010 (PERFIS FORMADOS A FRIO), NBR6123:2023 (AÇÃO DO VENTO) E NBR6120:2019 (SOBRECARGA DE USO).

TÍTULO: EIXO D

FORMATO: A1	ARQUIVO: PM-2604-POH-01-R00		Nº PROJETO	REVISÃO
ESCALA: 1:50	DATA: 23/04/26	PÁGINA: 1	2604	00

Tekla Structures

ESTE DOCUMENTO NÃO PODE SER REPRODUZIDO, INTEGRAL OU PARCIALMENTE, POR QUALQUER MEIO, INCLUINDO FOTOCÓPIA, SEM AUTORIZAÇÃO

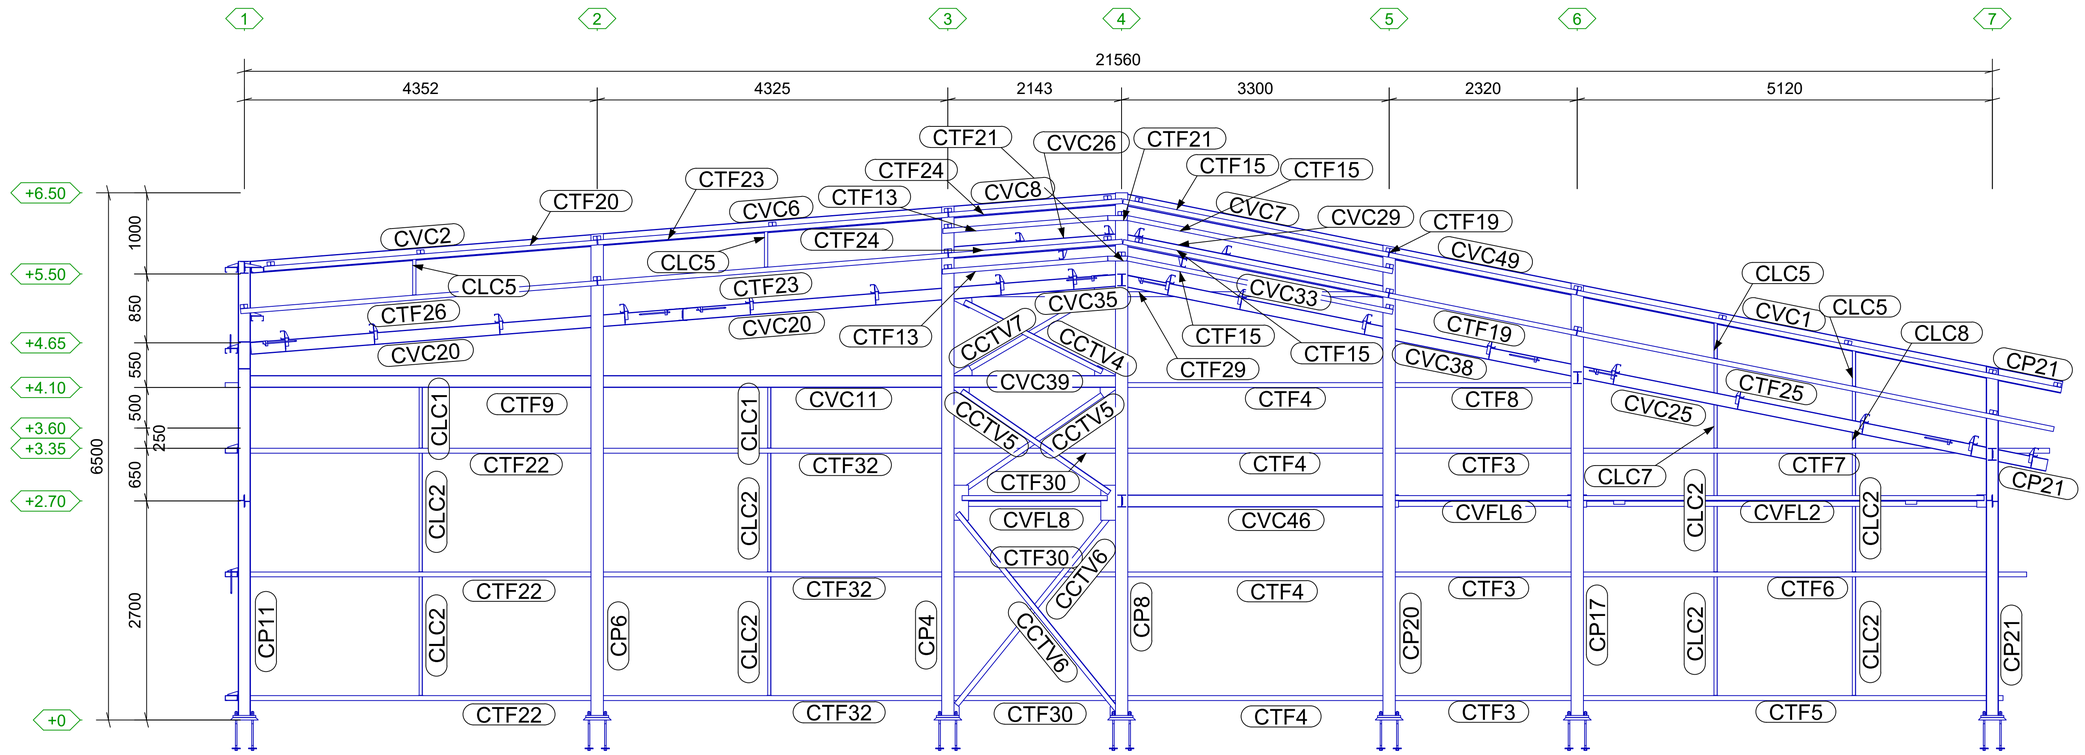

EIXO F
ESC.: 1:50

REV.	DATA	REVISOR	OBSERVAÇÕES
00	23/04/26	HELEN KÁSSIA	EMISSÃO INICIAL

STRUCKSTEEL
ESTRUTURAS METÁLICAS
strucksteelestruturasmetalicas@gmail.com

POSTO OPERACIONAL HIDROLÂNDIA

PROPRIETÁRIO:

PROJETISTA: CORPO DE BOMBEIROS MILITAR DE GOIÁS- CNPJ 33.638.099/0001-00

ENGº. JOÃO PEDRO GUIMARÃES BATISTELA - CREA 101.831.1009/D-GO

DESENHISTA:

ENGª. HELEN KÁSSIA PEREIRA SILVA - CREA 101.916.4573/D-GO

PROJETO ELABORADO SEGUINDO NORMAS VIGENTES - NBR8800:2024 (PERFIS LAMINADOS), NBR14762:2010 (PERFIS FORMADOS A FRIO), NBR6123:2023 (AÇÃO DO VENTO) E NBR8120:2019 (SOBRECARGA DE USO).

TÍTULO: EIXO F

FORMATO: A1	ARQUIVO: PM-2604-POH-01-R00		Nº PROJETO	REVISÃO
ESCALA: 1:50	DATA: 23/04/26	PÁGINA: 1	2604	00

Tekla Structures